


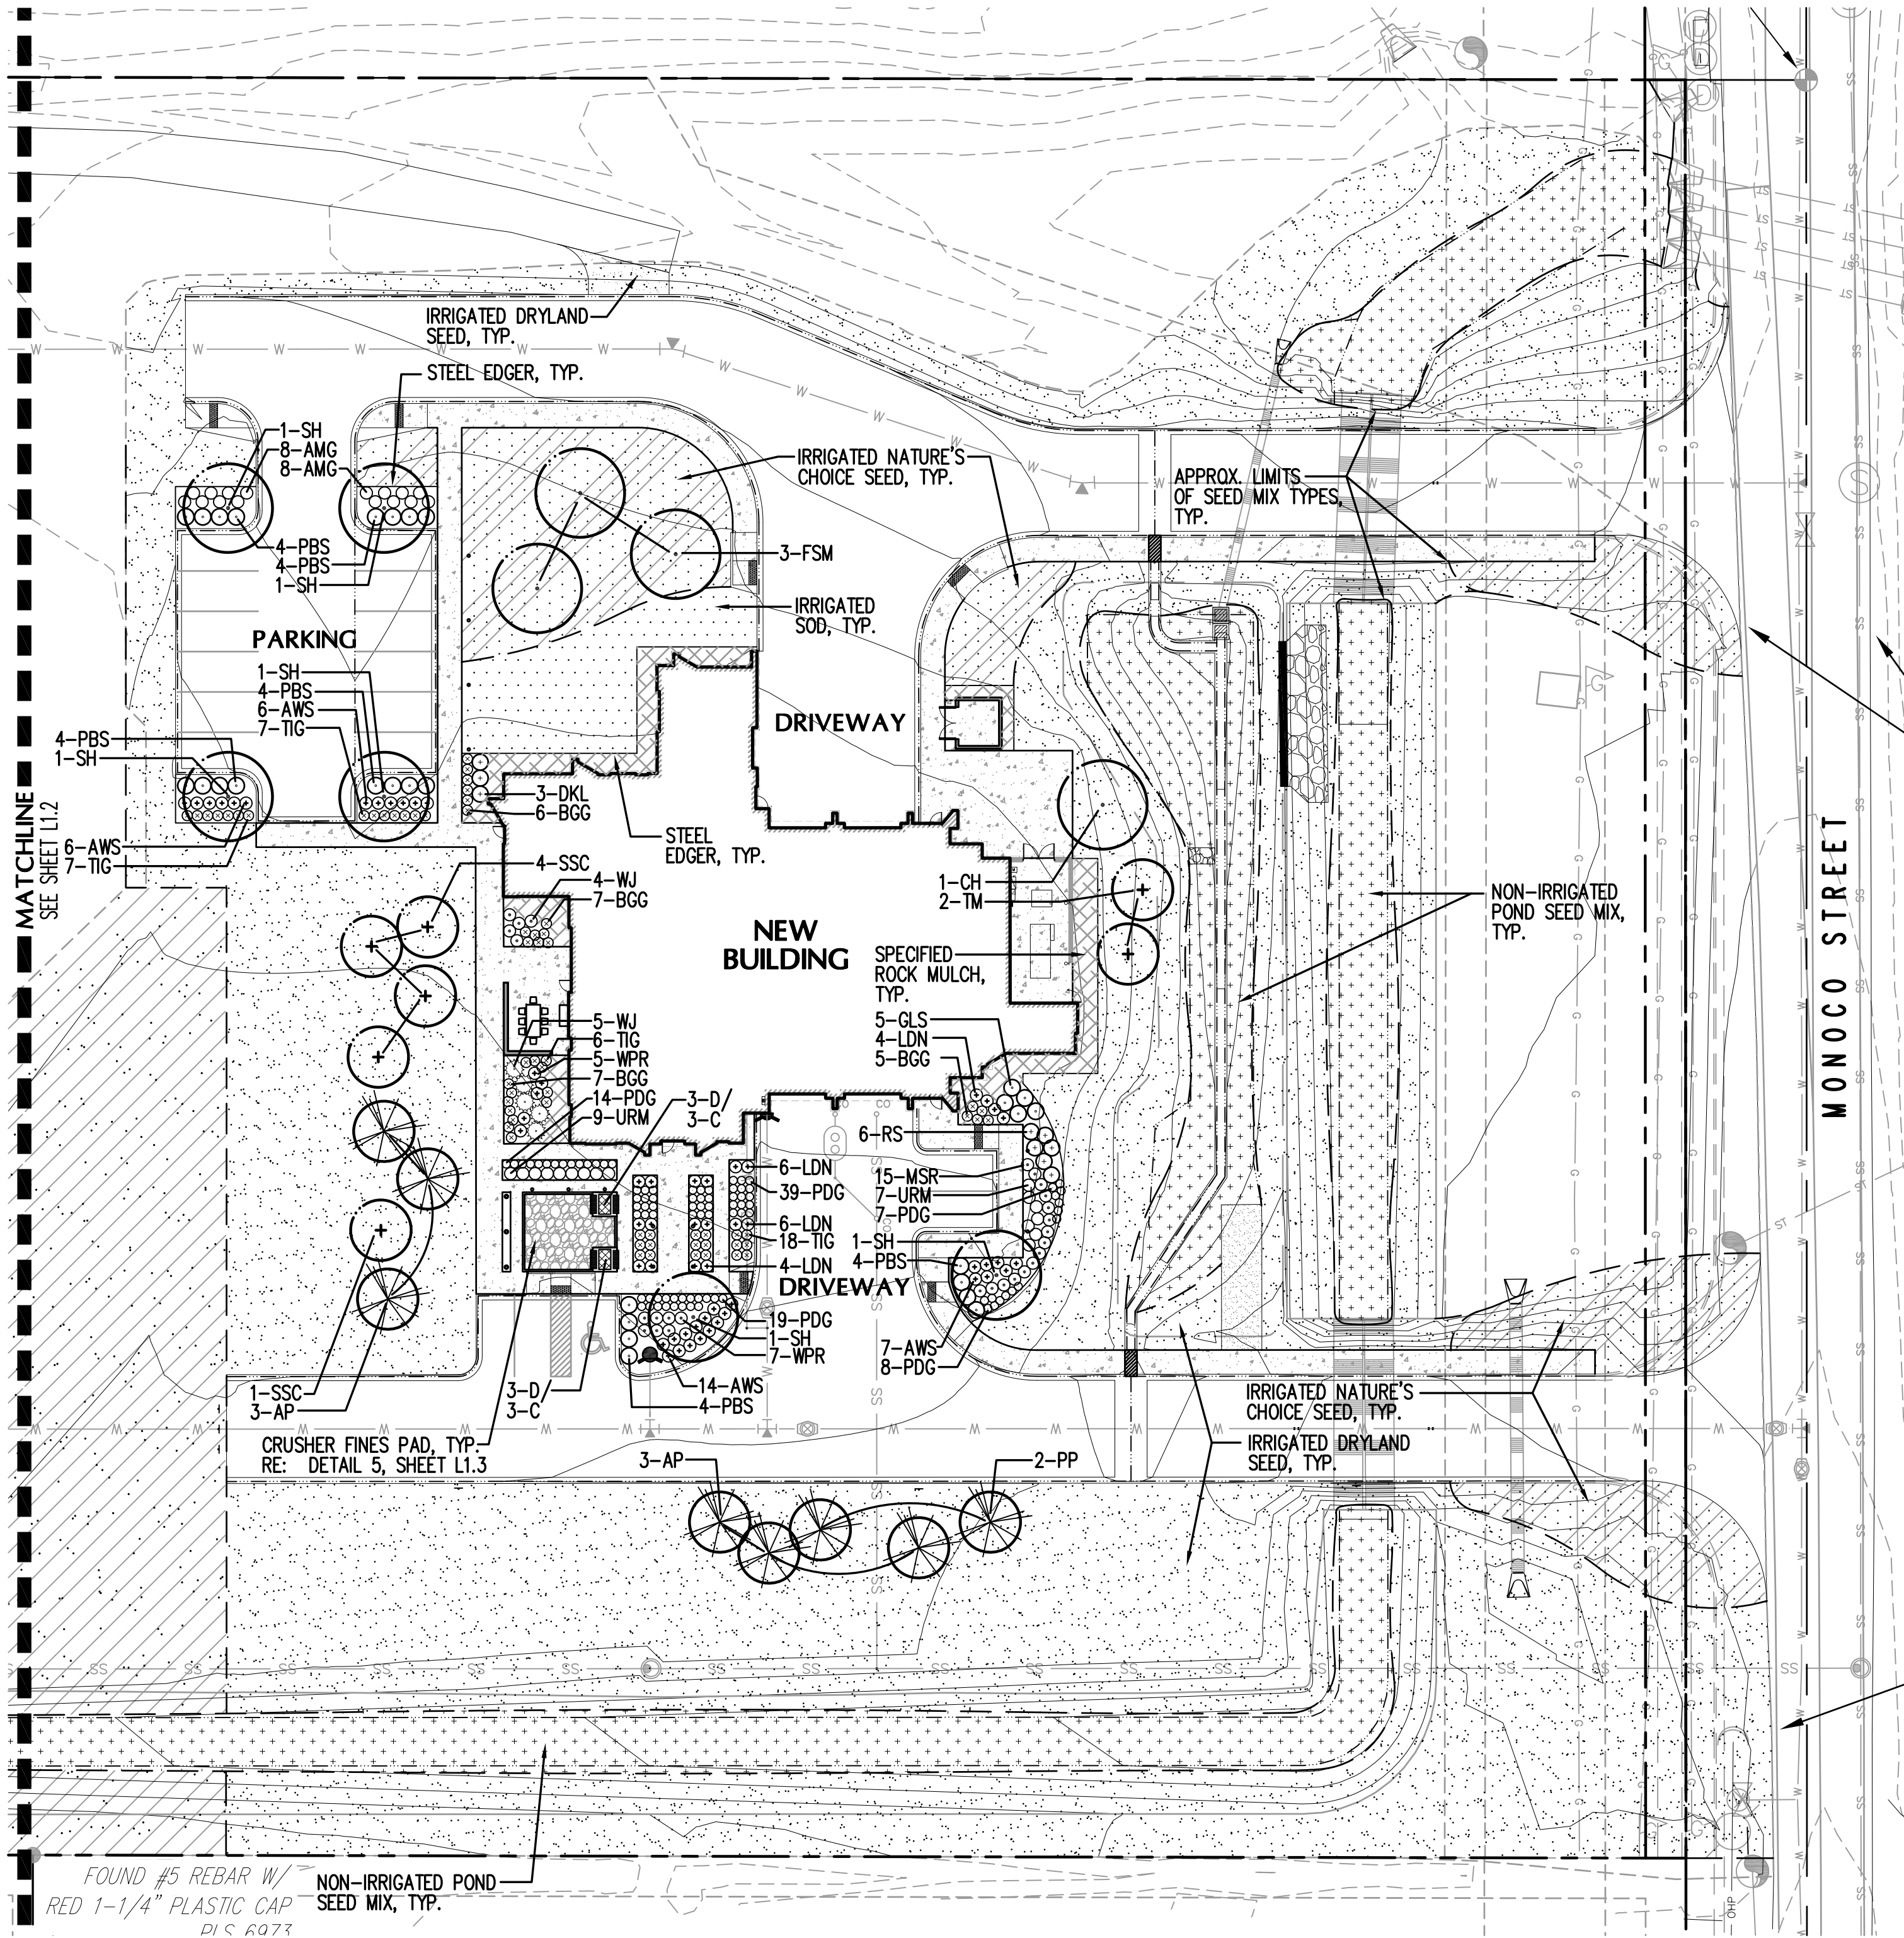

LANDSCAPE LEGEND

- NEW DECIDUOUS TREE
- NEW DECIDUOUS ORNAMENTAL TREE
- NEW EVERGREEN TREE
- NEW DECIDUOUS SHRUBS
- NEW EVERGREEN SHRUBS
- NEW ORNAMENTAL GRASSES
- NEW PERENNIALS
- EXISTING DECIDUOUS TREE TO REMAIN. SEE SHEET L1.2 FOR PROTECTION NOTES AND DETAILS
- EXISTING EVERGREEN TREE TO REMAIN. SEE SHEET L1.2 FOR PROTECTION NOTES AND DETAILS



GROUNDCOVER LEGEND

- IRRIGATED SOD
RE: CITY SPECIFICATIONS
- IRRIGATED SEED MIX (NATURE'S CHOICE)
SHEEPS FESCUE
EPHRAIM CRESTED WHEATGRASS
HARD FESCUE
SEEDING RATE: 4-5 LBS PLS/1,000 S.F. 15%
REFER TO LANDSCAPE NOTE #12, SHEET L1.2 FOR SEEDING INFORMATION. 15%
- IRRIGATED DRYLAND GRASS SEED MIX
BLUE GRAMA 29%
BUFFALOGRASS 25%
SIDOATS GRAMA 20%
WESTERN WHEATGRASS 20%
GREEN NEEDLEGRASS 5%
SAND DROPSEED 1%
SEEDING RATE: 40 LBS PLS/1 ACRE
- TEMP-IRRIGATED DRYLAND GRASS SEED MIX
BLUE GRAMA 29%
BUFFALOGRASS 25%
SIDOATS GRAMA 20%
WESTERN WHEATGRASS 20%
GREEN NEEDLEGRASS 5%
SAND DROPSEED 1%
SEEDING RATE: 40 LBS PLS/1 ACRE
- TEMP-IRRIGATED POND GRASS SEED MIX
SAND BLUESTEM 14%
SIDOATS GRAMA 15%
PRAIRIE SANDREED 15%
INDIAN RICEGRASS 10%
SWITCHGRASS 16%
WESTERN WHEATGRASS 10%
LITTLE BLUESTEM 10%
SAND DROPSEED 10%
SEEDING RATE: 28.5 LBS PLS/1 ACRE
- SPECIFIED 1"-1-1/2" 'HORIZON' RIVER ROCK MULCH OVER SPECIFIED FILTER FABRIC

PLANT LIST

SYM. COMMON/ BOTANIC NAME	SIZE	COMMENTS	WATER USE
DECIDUOUS SHADE TREES			
SH Shademaster Honeylocust <i>Gleditsia triacanthos</i> var. <i>inermis</i> 'Shademaster'	2 1/2" cal.	Specimen quality, full crown, B&B, staked	LOW
FSM Flashfire Sugar Maple <i>Acer saccharum</i> 'Flashfire'	2 1/2" cal.	Specimen quality, full crown, B&B, staked	MED
AE Accolade Elm <i>Ulmus</i> 'Accolade'	2 1/2" cal.	Specimen quality, full crown, B&B, staked	LOW
CH Chicagoland Hackberry <i>Celtis occidentalis</i> 'Chicagoland'	2 1/2" cal.	Specimen quality, full crown, B&B, staked	LOW
ORNAMENTAL TREES			
PCC Chanticleer Pear <i>Pyrus calleryana</i> 'Chanticleer'	2" cal.	Specimen quality, full crown, B&B, staked	MED
SSC Spring Snow Crabapple <i>Malus</i> sp. 'Spring Snow'	2" cal.	Specimen quality, full crown, B&B, staked	LOW
TM Tatarian Maple <i>Acer tataricum</i>	2" cal.	Specimen quality, clump form, B&B, staked	LOW
EVERGREEN TREES			
AP Austrian Pine <i>Pinus nigra</i>	6' ht.-8' ht.	Specimen quality, full form, B&B, guyed	LOW
PP Pinon Pine <i>Pinus cembroides</i> <i>edulis</i>	6' ht.-8' ht.	Specimen quality, full form, B&B, guyed	LOW
DECIDUOUS SHRUBS			
AWS Anthony Waterer Spirea <i>Spiraea</i> 'Anthony Waterer'	5 gal.	container, 5 canes min. 36" ht., plant 3' o.c.	MED
LDN Little Devil Ninebark <i>Physocarpus opulifolius</i> 'Little Devil'	5 gal.	container, 5 canes min. 36" ht., plant 3' o.c.	LOW
WPR Winnipeg Parks Rose <i>Rosa</i> 'Winnipeg Parks'	5 gal.	container, 5 canes min. 36" ht., plant 3' o.c.	LOW
MSR Morden Sunrise Rose <i>Rosa</i> 'Morden Sunrise'	5 gal.	container, 5 canes min. 30" ht., plant 3' o.c.	LOW
DKL Dwarf Korean Lilac <i>Syringa meyeri</i> 'Palibin'	5 gal.	container, 5 canes min. 4' ht., plant 4' o.c.	LOW
RS Russian sage <i>Perovskia atriplicifolia</i>	5 gal.	container, 5 canes min. 4' ht., plant 4' o.c.	LOW
PBS Pawnee Buttes Sandcherry <i>Prunus Besseyi</i> 'Pawnee Buttes'	5 gal.	container, 5 canes min. 2' ht., plant 4' o.c.	LOW
GLS Grow Low Creeping Sumac <i>Rhus trilobata</i> 'Autumn Amber'	5 gal.	container, 5 canes min. 18" ht., plant 4' o.c.	LOW
GBC Gwen's Buffalo Currant <i>Ribes aureum</i> 'Gwen's Buffalo'	5 gal.	container, 5 canes min. 5' ht., plant 4' o.c.	LOW
TP Tidy Peashrub <i>Caragana microphylla</i> 'Tidy'	5 gal.	container, 5 canes min. 6' ht., plant 4' o.c.	LOW
EVERGREEN SHRUBS			
WJ Wilton Juniper <i>Juniperus horizontalis</i> 'Wiltonii'	5 gal.	container, 18"-24" spread plant 4' o.c.	LOW
PERENNIALS/ORNAMENTAL GRASSES			
D Stella de Oro Daylily <i>Memorocallis</i> 'Stella de Oro'	1 gal.	container, plant 18" o.c.	LOW
C Faassen's Catmint <i>Nepeta x faassenii</i>	1 gal.	container, plant 30" o.c.	LOW
PDG Prairie Dropseed Grass <i>Sporobolus heterolepis</i>	1 gal.	container, plant 24" o.c.	LOW
TIG Thin Man Indian Grass <i>Sorghastrum nutans</i> 'Thin Man'	1 gal.	container, plant 30" o.c.	LOW
BGG Blue Grama Grass <i>Bouteloua gracilis</i> 'Blond Ambition'	1 gal.	container, plant 30" o.c.	LOW
AMG Adagio Maiden Grass <i>Miscanthus sinensis</i> 'Adagio'	1 gal.	container, plant 36" o.c.	LOW
URM Undaunted Ruby Muhly <i>Muhlenbergia reverchonii</i> 'Undaunted'	1 gal.	container, plant 36" o.c.	LOW

REFER TO SHEET L1.3 FOR
LANDSCAPE NOTES,
AND DETAILS

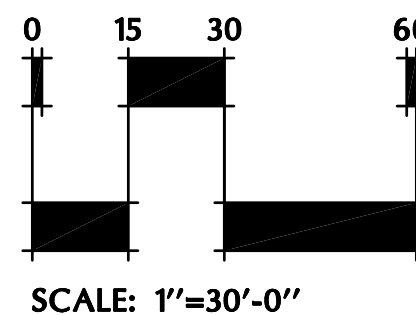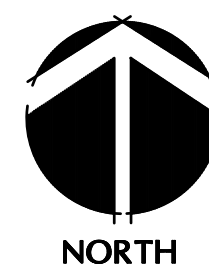

meuran
designgroup
site design
landscape architecture
site planning
700 colorado boulevard, suite 131
denver, colorado 80206
303.512.0549 www.meuran.com



UNCC Know what's below.
UTILITY NOTIFICATION
CENTER OF COLORADO
Call before you dig.

CALL 811 2-BUSINESS DAYS IN ADVANCE
BEFORE YOU DIG, GRADE OR EXCAVATE FOR
MARKING OF UNDERGROUND MEMBER UTILITIES

MEURAN DESIGN GROUP ASSUMES NO RESPONSIBILITY FOR UTILITY
LOCATIONS. THE UTILITIES SHOWN ON THIS DRAWING HAVE BEEN
PLOTTED FROM THE BEST AVAILABLE INFORMATION. IT IS,
HOWEVER, THE CONTRACTORS RESPONSIBILITY TO FIELD VERIFY THE
SIZE, MATERIAL, HORIZONTAL AND VERTICAL LOCATION OF ALL
UTILITIES PRIOR TO THE COMMENCEMENT OF ANY CONSTRUCTION.

ALLRED & ASSOCIATES

ARCHITECTURE | PLANNING | INTERIOR DESIGN
590 BURBANK ST. SUITE 125, BROOMFIELD, CO 80020 PHONE: 303.465.4392 FAX: 303.465.4392
www.allredandassociates.com


BID SET | JOB NO. 24.100

CITY OF THORNTON

FIRE STATION #8

15343 MONACO STREET

THORNTON, COLORADO 80602

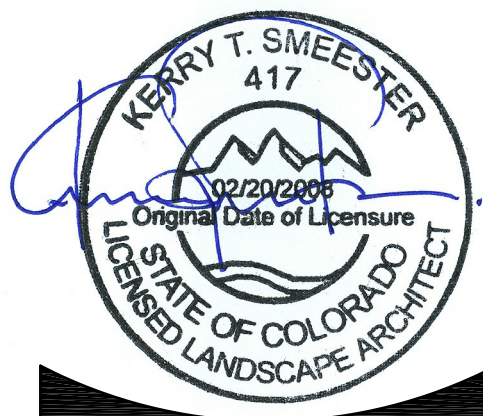


REVISION NAME	DATE

ISSUE DATE: 2024 0927

LANDSCAPE PLAN


L1.1

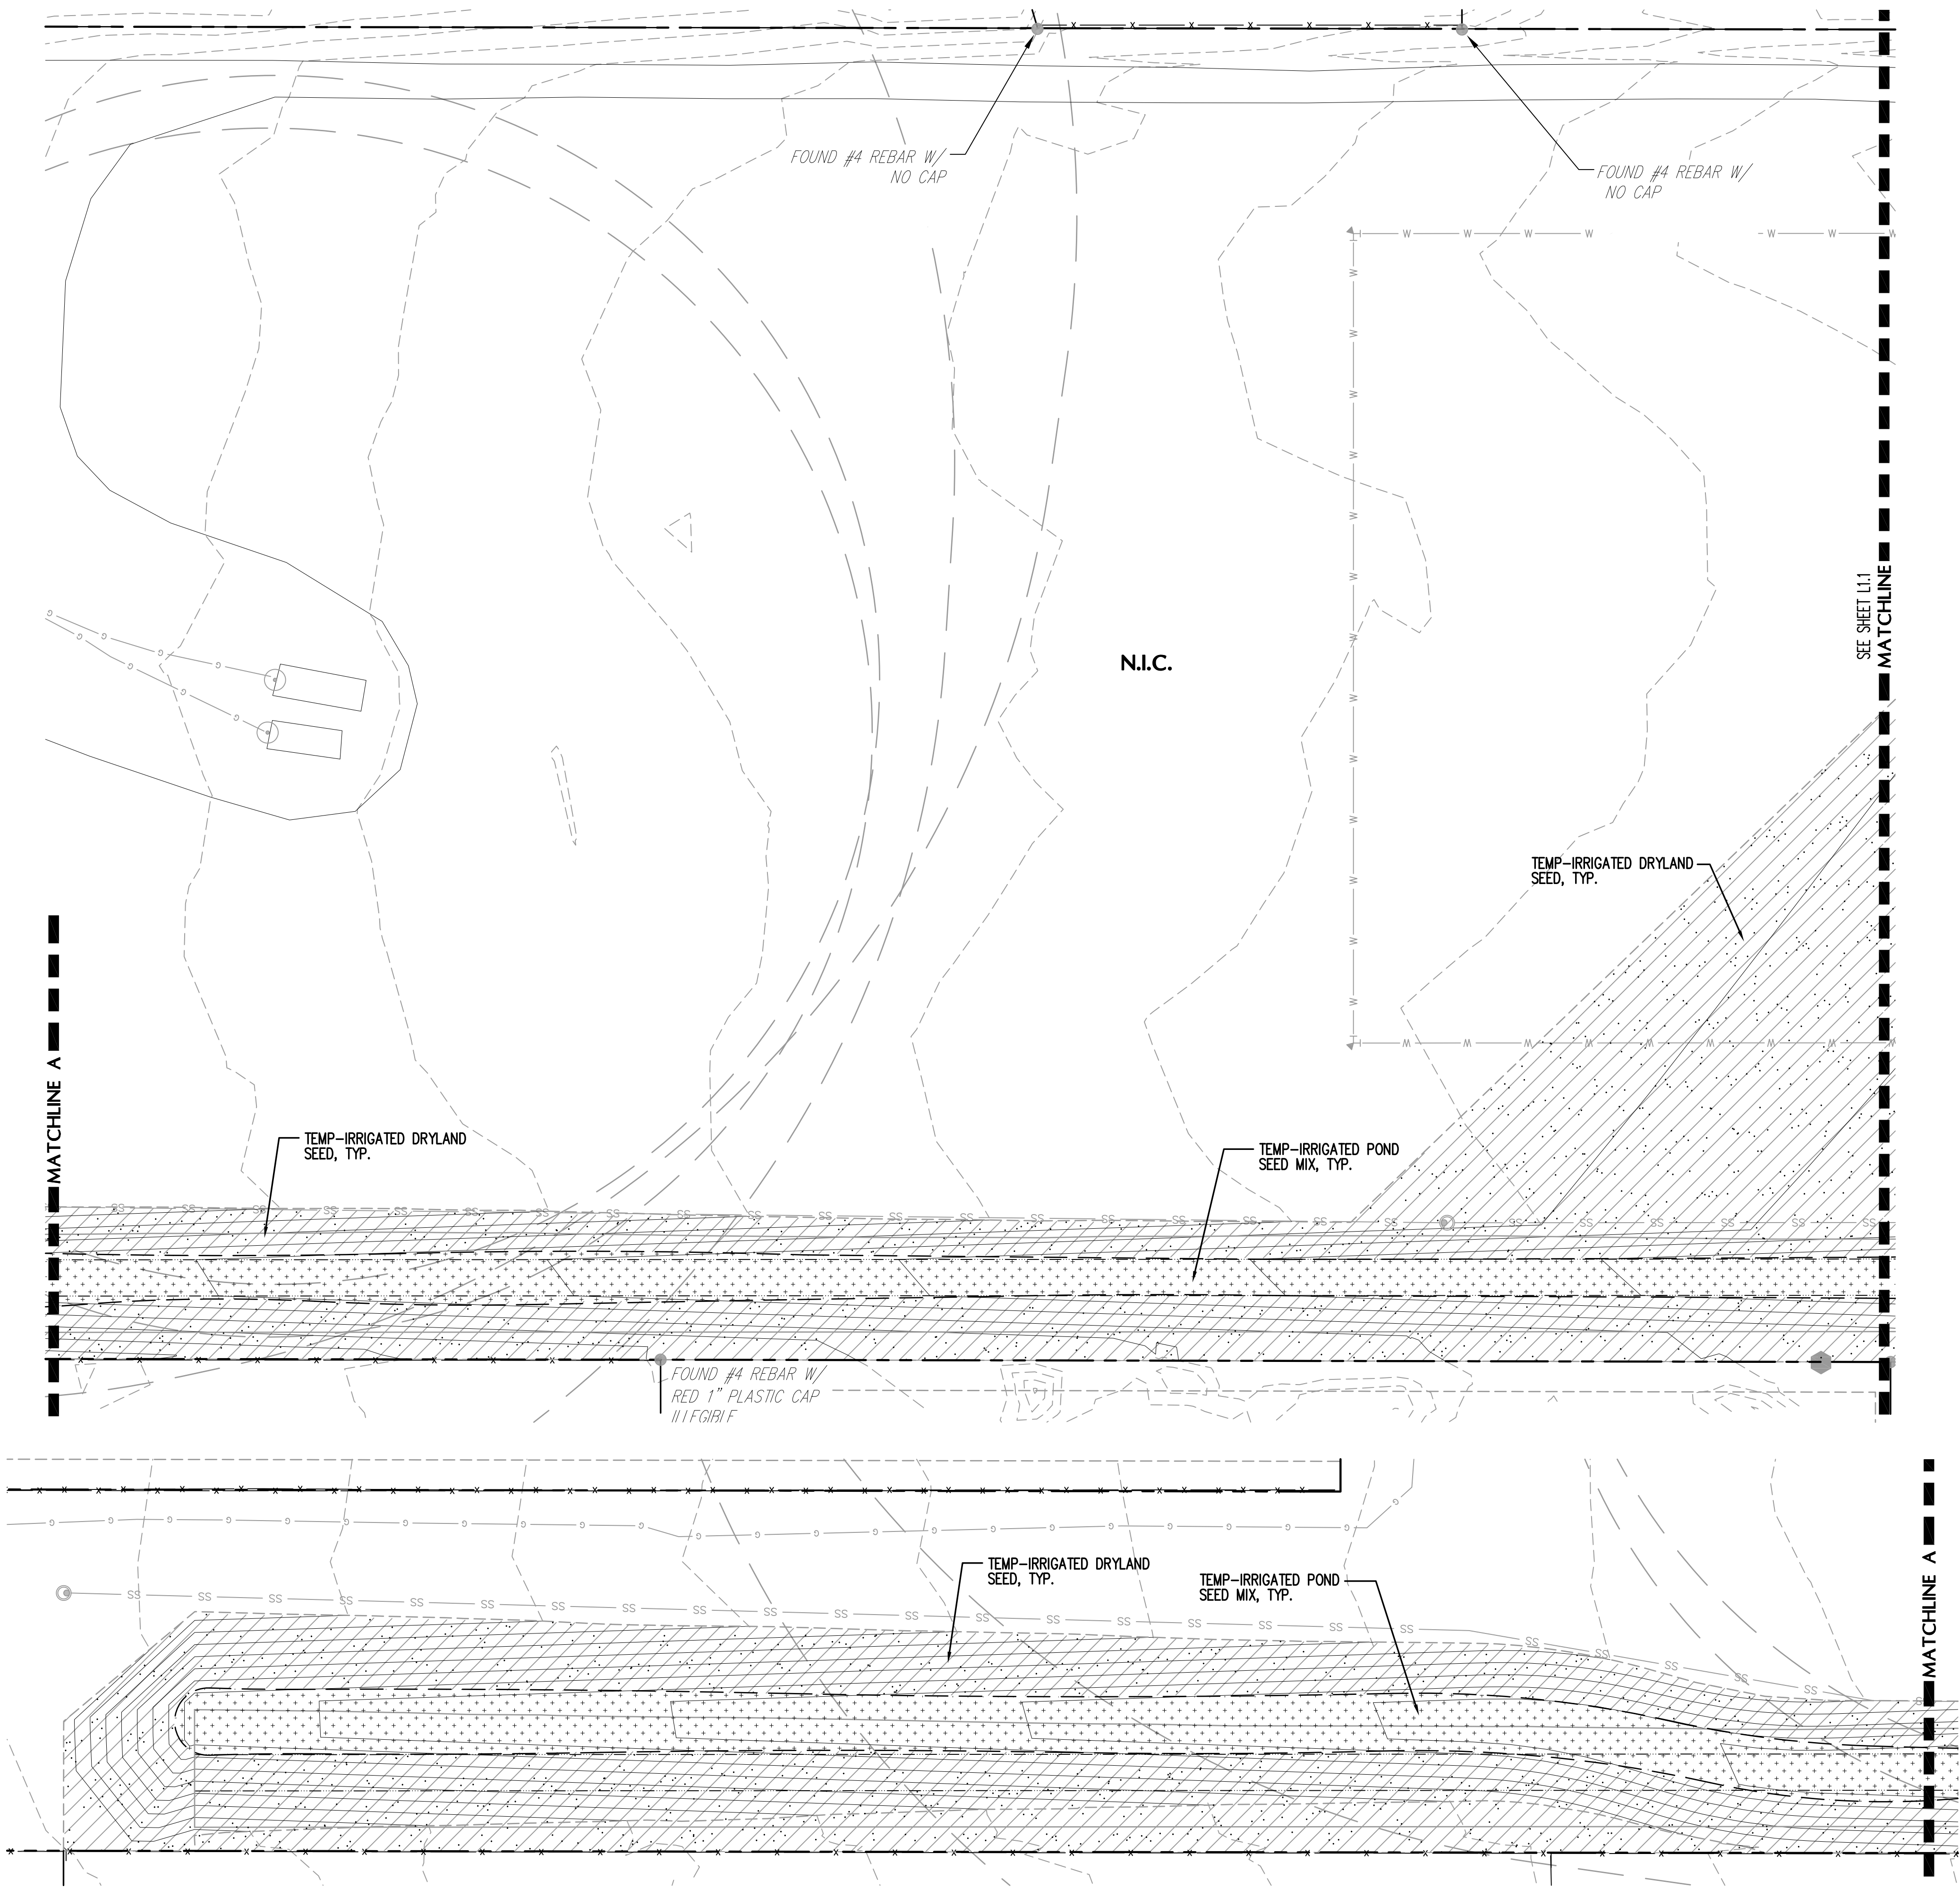


GROUND COVER LEGEND



IRRIGATED DRYLAND GRASS SEED MIX	
BLUE GRAMA	29%
BUFFALOGRASS	25%
SIDEOATS GRAMA	20%
WESTERN WHEATGRASS	20%
GREEN NEEDLEGRASS	5%
SAND DROPSEED	1%
SEEDING RATE: 40 LBS PLS/1 ACRE	

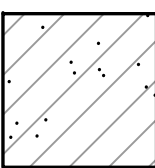

TEMP-IRRIGATED DRYLAND GRASS SEED MIX	
BLUE GRAMA	29%
BUFFALOGRASS	25%
SIDEOATS GRAMA	20%
WESTERN WHEATGRASS	20%
GREEN NEEDLEGRASS	5%
SAND DROPSEED	1%
SEEDING RATE: 40 LBS PLS/1 ACRE	

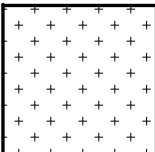

TEMP-IRRIGATED POND GRASS SEED MIX	
SAND BLUESTEM	14%
SIDEOATS GRAMA	10%
PRAIRIE SANDREED	10%
INDIAN RICEGRASS	10%
SWITCHGRASS	16%
WESTERN WHEATGRASS	10%
LITTLE BLUESTEM	10%
ALKALI SACATON	10%
SAND DROPSEED	10%
SEEDING RATE: 28.5 LBS PLS/1 ACRE	

REFER TO SHEET L 1.3 FOR
LANDSCAPE NOTES,
AND DETAILS



UNCC Know what's below.
UTILITY NOTIFICATION CENTER OF COLORADO Call before you dig.





CALL 811 2-BUSINESS DAYS IN ADVANCE
BEFORE YOU DIG, GRADE OR EXCAVATE FOR
MARKING OF UNDERGROUND MEMBER UTILITIES

MEURAN DESIGN GROUP ASSUMES NO RESPONSIBILITY FOR UTILITY LOCATIONS. THE UTILITIES SHOWN ON THIS DRAWING HAVE BEEN PLOTTED FROM THE BEST AVAILABLE INFORMATION. IT IS, HOWEVER, THE CONTRACTORS RESPONSIBILITY TO FIELD VERIFY THE SIZE, MATERIAL, HORIZONTAL AND VERTICAL LOCATION OF ALL UTILITIES PRIOR TO THE COMMENCEMENT OF ANY CONSTRUCTION.

meuran
designgroup

site design
landscape architecture
site planning
700 colorado boulevard, suite 131
denver, colorado 80206
303.512.0549 www.meuran.com

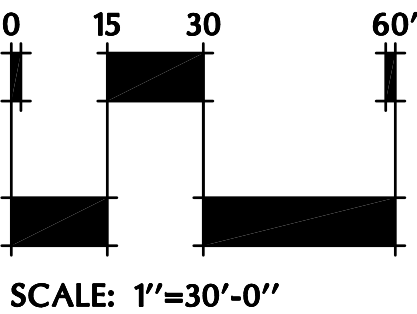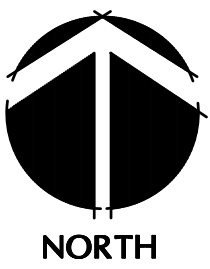

ALLRED & ASSOCIATES

ARCHITECTURE | PLANNING | INTERIOR DESIGN

590 BURBANK ST. SUITE 125, BROOMFIELD, CO 80020 PHONE: 303.465.4392 FAX: 303.465.4392 www.allredarch.com


BID SET | JOB NO. 24.100

CITY OF THORNTON

FIRE STATION #8

15343 MONACO STREET

THORNTON, COLORADO 80602

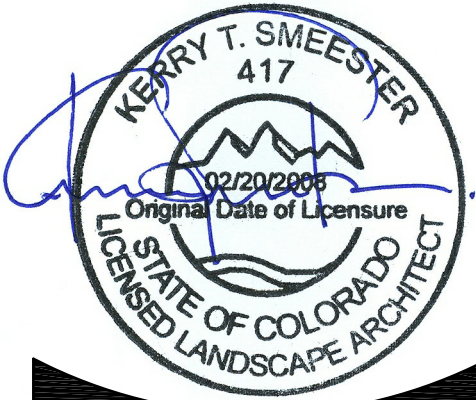

REVISION NAME	DATE

ISSUE DATE: 2024 0927

LANDSCAPE PLAN

L1.2

STAKING: INSTALL 6" METAL T-POST STAKES OUTSIDE PLANTING PIT IN UNDISTURBED MULCHED SOIL. USE #12 GAUGE GALVANIZED WIRE.



ALLOW FOR SOME TRUNK MOVEMENT

ATTACH TO 2" NYLON STRAPS THROUGH METAL CROMMETS, WITH 1/2" x 15" WHITE PVC SLEEVE ON EACH WIRE.

NYLON STRAPS SHALL BE LONG ENOUGH TO ACCOMMODATE 1-1/2" OF TRUNK GROWTH.

ADD PROTECTOR CAP TO TOP OF POST.

WRAP TREES TO FIRST BRANCH IF PLANTED IN THE FALL. DO NOT WRAP IF PLANTED IN SPRING.

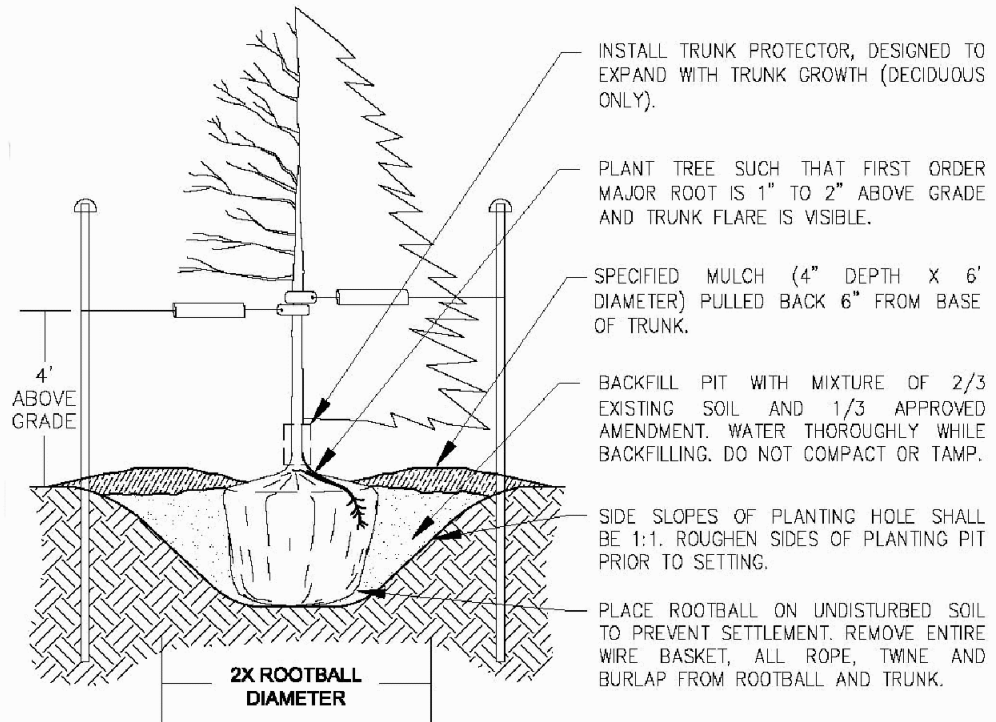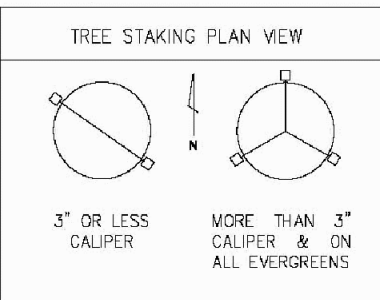


1 DECIDUOUS TREE PLANTING N.T.S.

PLANT SHRUBS 1/2 MATURE WIDTH OR 4' FROM EDGE OF WALK, CURB OR EDGING.


ENTIRE SHRUB BED AREA SHALL BE AMENDED WITH 4 CUBIC YARDS (6 CUBIC YARDS FOR CITY MAINTAINED PROJECTS) OF CLASS I OR CLASS II COMPOST PER 1000 S.F. TILLED TO DEPTH OF 8".

IF PLANT IS ROOT BOUND AND HAS CIRCLING ROOTS, SHEAR 1/2" OF THE ROOTMASS OFF OF ALL SIDES AND BOTTOM.


DO NOT PLANT SHRUBS HIGHER THAN SURROUNDING GRADE. BACKFILL SOIL SHOULD BE PULLED OVER TOP OF ROOTBALL (NO MORE THAN 1") TO PREVENT MOISTURE WICKING AND TO ALLOW ROOTS TO GROW INTO SURROUNDING SOIL.

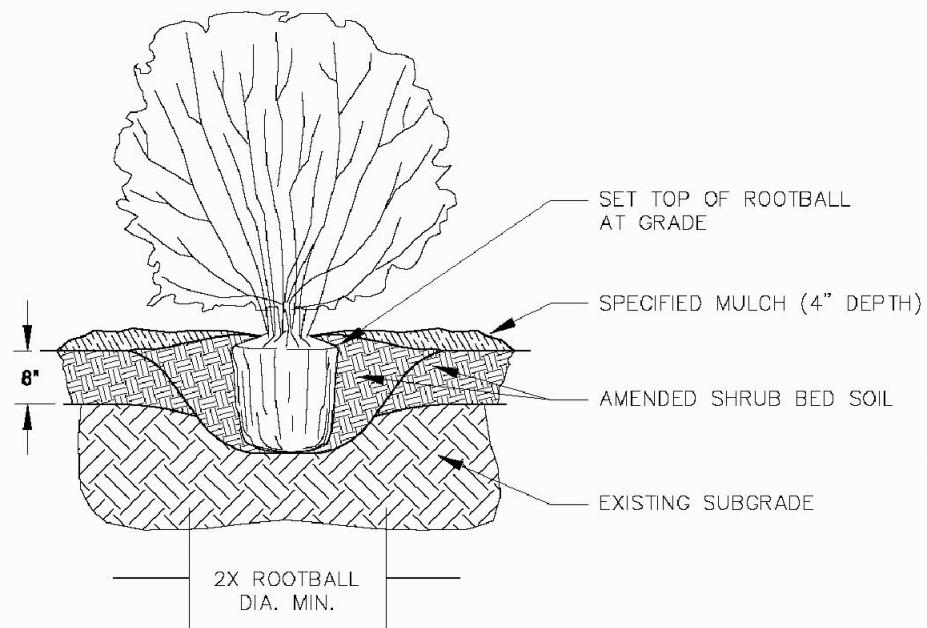


2 SHRUB PLANTING DETAIL N.T.S.

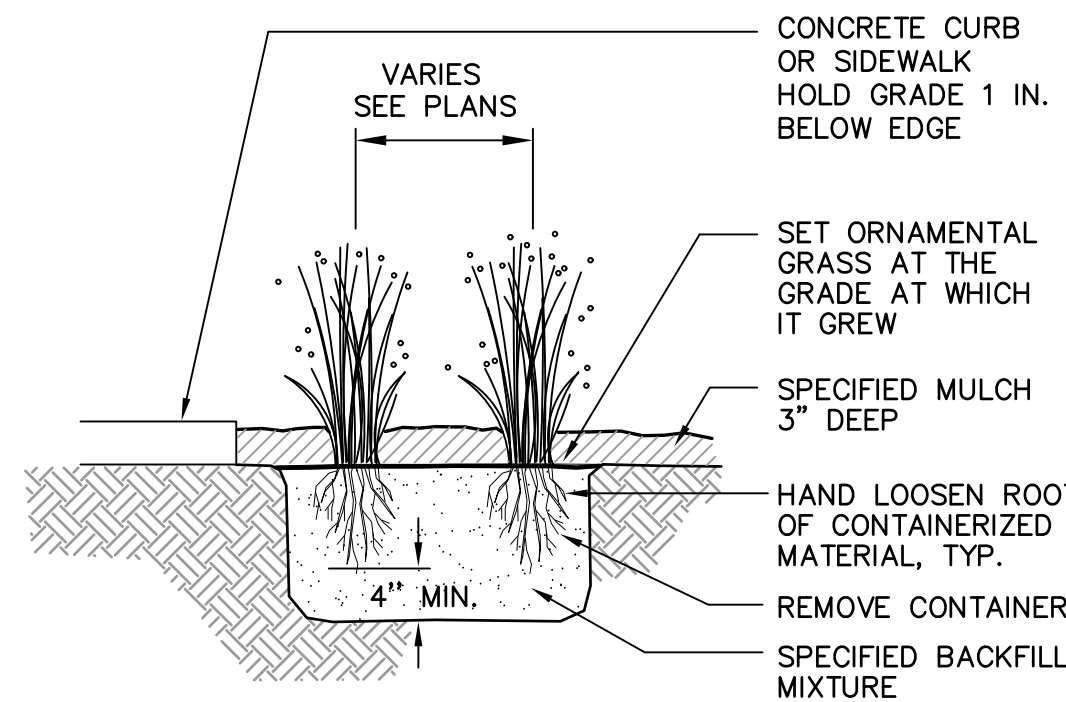

3 ORNAMENTAL GRASS DETAIL N.T.S.

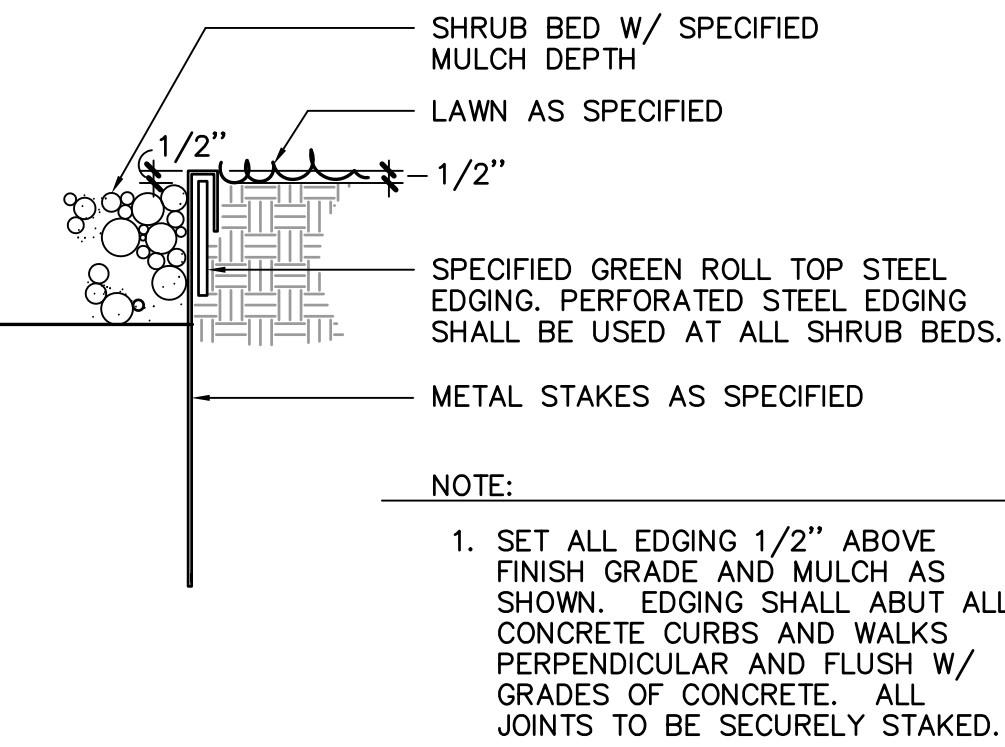


4 STEEL EDGER DETAIL N.T.S.

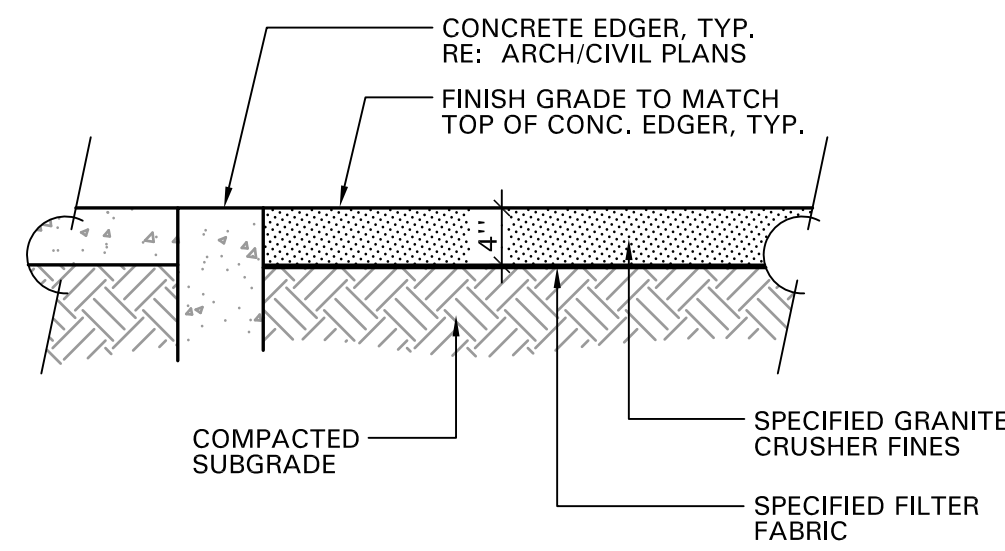

NOTES:
CRUSHER FINES TO BE TAN IN COLOR. SUBMIT SAMPLE FOR CITY APPROVAL.
CRUSHER FINES TO BE STABILIZED BY A CITY APPROVED POLYMER.

5 CRUSHER FINES PAD N.T.S.

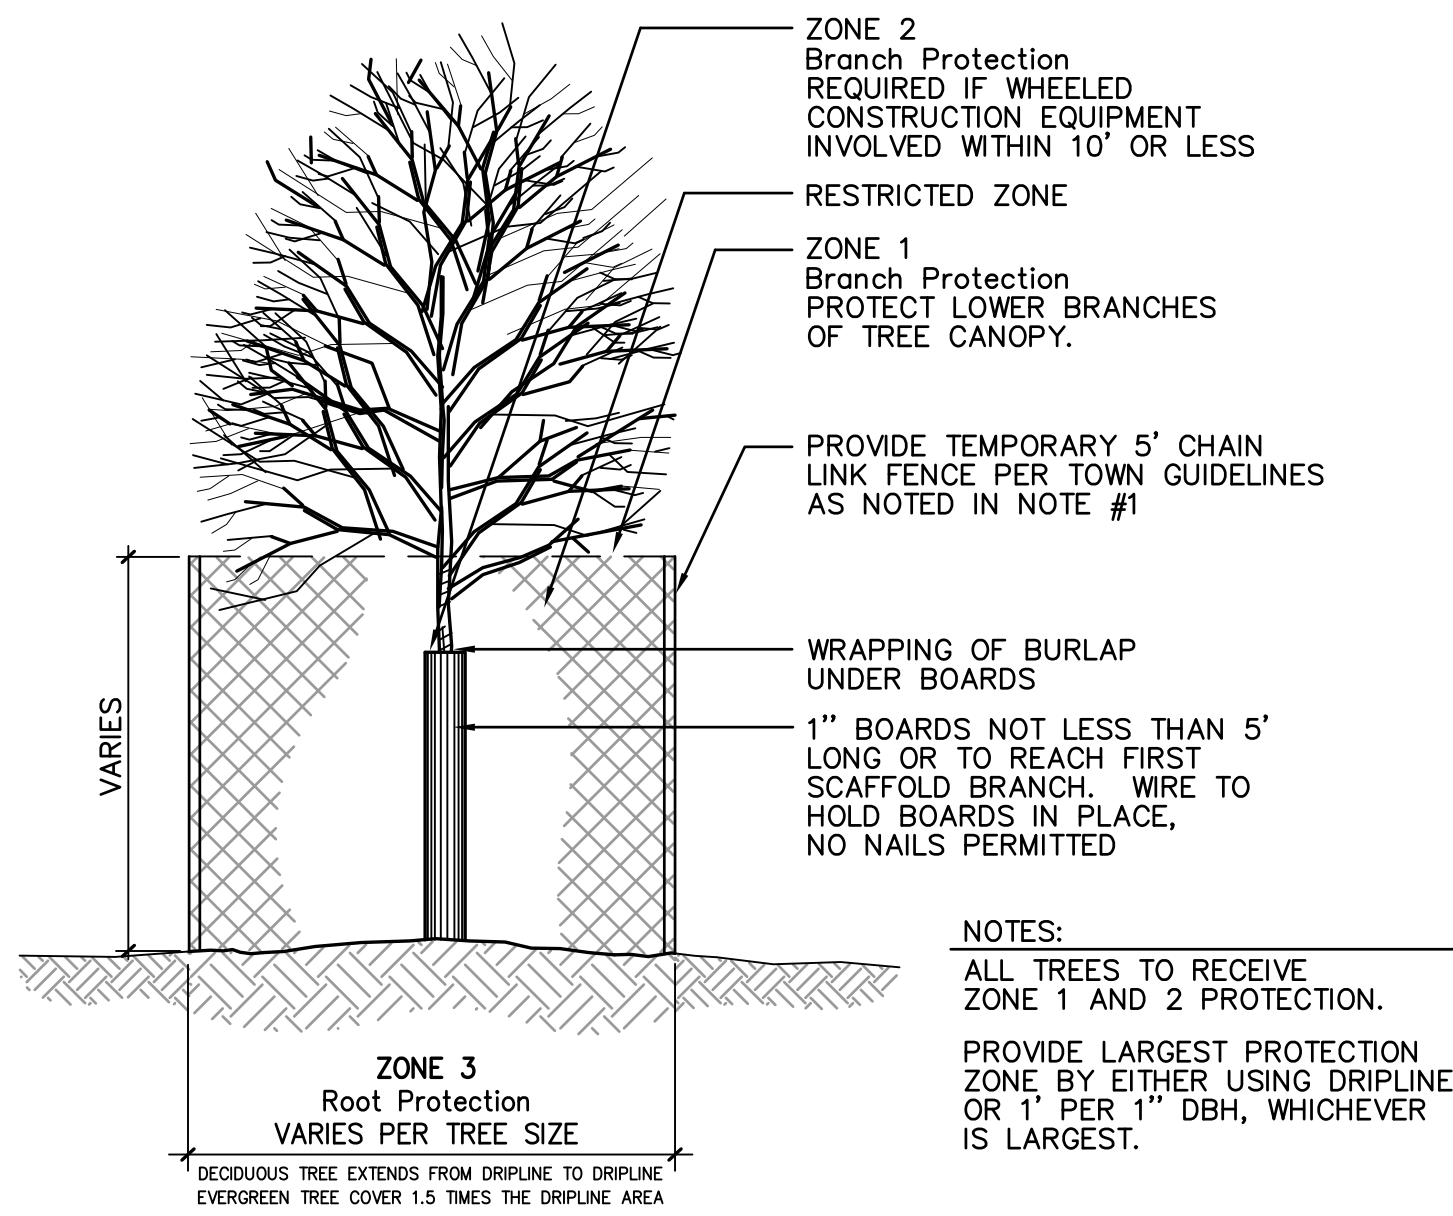

6 EXISTING TREE PROTECTION N.T.S.

TREE PRESERVATION AND REMOVAL NOTES:

- BARRICADES SHALL HAVE A 1-FOOT RADIUS PER INCH OF TRUNK DIAMETER, WITH A WOOD CHIP MULCH 6 TO 8 INCHES DEEP EXTENDING BEYOND THE BARRIER TO THE DRIPLINE, IF NEEDED. IF LOW BRANCHES WILL BE KEPT, PLACE THE FENCE OUTSIDE THE DRIPLINE. EXAMINE TREES AND BARRICADES AT LEAST ONCE A WEEK DURING CONSTRUCTION. WITHIN THE DRIP LINE OF PROTECTED EXISTING TREES, THERE SHALL BE NO CUT OR FILL UNLESS THE CONSULTING ARBORIST HAS EVALUATED AND APPROVED THE DISTURBANCE.
- ALL EXISTING PRESERVED SPRUCE TREES SHALL BE TREATED FOR IPS BEETLES TWICE PER YEAR (MARCH AND JULY).
- ALL TRENCHING, BORING, AND PUSHING OF UTILITIES THROUGH THE ROOT ZONES OF EXISTING SHALL BE AVOIDED.
- IF DAMAGE OCCURS TO ROOTS OF EXISTING TREES, THE ROOTS SHALL BE PRUNED AND COVERED WITH SOIL OR MOIST BURLAP WITHIN TWO HOURS.
- EARTHWORK SHALL NOT BE PLACED ADJACENT TO TREE TRUNKS.
- ALL CONSTRUCTION ACTIVITY SHALL BE PROHIBITED WITHIN THE FENCED ROOT/DRIPLINE IN ORDER TO PREVENT SOIL COMPACTION AS MUCH AS POSSIBLE.
- NO CONSTRUCTION RELATED WASH-OUT (E.G., LIME, ACID, CONCRETE) SHOULD OCCUR WITHIN 30 FEET OF ANY TREE TRUNK.
- A CERTIFIED ARBORIST SHALL PRUNE ALL EXISTING PRESERVED TREES.
- SUPPLEMENTAL WATERING IS RECOMMENDED DURING GROWING SEASON IF IRRIGATION SYSTEM IS NOT OPERABLE.
- EXISTING TREES #22, #23, #24, #25 AND #26 SHALL BE REMOVED AFTER THREE (3) GROWING SEASONS IF SIGNS OF DIEBACK OCCURS ON 1/3 OF THE TREE OR GREATER. THE CITY SHALL REPLACE WITH TREES MEETING THE REQUIREMENTS OF THE CITY OF THORNTON.

LANDSCAPE NOTES

- A PRE-CONSTRUCTION MEETING IS REQUIRED WITH THE CITY LANDSCAPE ARCHITECT PRIOR TO LANDSCAPE CONSTRUCTION.
- ALL LANDSCAPE AND IRRIGATION INSTALLATION SHALL CONFORM TO THE CITY STANDARDS AND SPECIFICATIONS, CHAPTER 800, AND THE CITY PARKS AND RECREATION SPECIFICATIONS.
- THIS LANDSCAPE ARCHITECTURAL SITE PLAN IS TO BE USED IN CONJUNCTION WITH THE CIVIL, MECHANICAL, ELECTRICAL AND ARCHITECTURAL SITE PLANS TO FORM COMPLETE INFORMATION REGARDING THIS SITE.
- ALL DECIDUOUS AND EVERGREEN TREES ARE TO BE TAGGED AT NURSERY BY THE OWNER'S REPRESENTATIVE PRIOR TO INSTALLATION. ANY PLANT NOT MEETING THE REPRESENTATIVE'S AND/OR CITY INSPECTOR'S APPROVAL WILL BE REJECTED AT ANY TIME PRIOR TO FINAL ACCEPTANCE.
- ALL TREES TO BE STAKED OR GUYED AS PER PLANT LIST AND DETAILS. ALL TREES IN TURF AREAS SHALL HAVE 8' MULCH RING WITH 4" DEPTH SPECIFIED WOOD MULCH. SEE DETAILS AND SPECIFICATIONS.
- ALL TREE AND SHRUB BED LOCATIONS ARE TO BE STAKED OUT ON SITE FOR APPROVAL BY THE OWNER'S REPRESENTATIVE PRIOR TO INSTALLATION.
- ALL SHRUB BEDS AND AREAS ADJACENT TO THE BUILDING SHALL BE MULCHED WITH 3" DEPTH 1"-1 1/2" 'HORIZON' RIVER ROCK MULCH. PLACE FILTER FABRIC UNDER ALL ROCK MULCH.
- ALL PERENNIAL BEDS SHALL BE MULCHED WITH 4" DEPTH DOUBLE SHREDDED WESTERN CEDAR WOOD MULCH. DO NOT PLACE FILTER FABRIC UNDER WOOD MULCH.
- ALL SHRUB BEDS AND MULCH AREAS ARE TO BE CONTAINED WITH ROLL TOP GREEN STEEL EDGER (NOT REQUIRED AT CURB, WALKS OR BUILDING). ROLL TOP STEEL EDGER SHALL BE USED TO SEPARATE WOOD AND ROCK MULCHES.
- ALL NEW LANDSCAPE AREAS INCLUDING SODDED AREAS SHALL BE ROTOTILLED WITH CLASS 1 COMPOST AT THE RATE OF 6 CUBIC YARDS PER 1,000 SQUARE FEET. THIS PREPARATION SHALL BE THOROUGHLY INCORPORATED INTO THE TOP 8" OF SOIL.
- REFER TO CITY SPECIFICATIONS FOR IRRIGATED SOD TYPE.
- REFER TO SHEET L1.1 FOR IRRIGATED AND NON-IRRIGATED SEED MIXES AND APPLICATION RATES. ALL AREAS TO BE SEEDED SHALL MEET CITY DESIGN GUIDELINES INCLUDING HAVE WEEDS CHEMICALLY ERADICATED AND SHALL BE FREE OF WEEDS PRIOR TO SEEDING. CITY REQUIRES AN INSPECTION OF SEED BED PRIOR TO SEEDING.
- ALL LANDSCAPE AREAS INCLUDING THE IRRIGATED SEEDING WILL BE WATERED BY AN UNDERGROUND AUTOMATIC IRRIGATION SYSTEM. THE IRRIGATION SYSTEM SHALL MEET ALL CITY DESIGN AND INSPECTION REQUIREMENTS.
- IRRIGATION CONSTRUCTION DRAWINGS PREPARED BY AN IRRIGATION ASSOCIATION CERTIFIED IRRIGATION DESIGNER WILL BE SUBMITTED TO THE CITY FOR FINAL APPROVAL PRIOR TO INSTALLATION.
- ESTABLISHMENT IRRIGATION USUALLY MEANS APPLYING WATER A MINIMUM OF 2 TIMES/DAY UNTIL SEED GERMINATES TO THE THREE-LEAF STAGE. AFTER THE THREE-LEAF STAGE AND UNTIL THE GRASS IS 3"-4" TALL, WATER TWO TIMES/DAY WITH A TOTAL 3/10" WATER APPLIED/DAY.
- AFTER THE FIRST MOWING, GENERALLY APPLY 1" EVERY TWO WEEKS. ADJUST ESTABLISHMENT IRRIGATION INCHES BY NATURAL PRECIPITATION AMOUNTS.
- TREES LOCATED WITHIN SIGHT TRIANGLES SHALL BE PRUNED BETWEEN 2.5 FT AND 8 FT AS MEASURED FROM TOP OF CURB, TYPICAL.
- PLEASE REFER TO THE CITY OF THORNTON STANDARDS AND SPECIFICATIONS FOR INFORMATION REGARDING PRESERVATION OF EXISTING TREES.
- ALL AREAS DISTURBED REGARDLESS OF BEING SHOWN DIFFERENTLY ON THE APPROVED PLANS OR AREAS DISTURBED OFF THE PROPERTY SHALL HAVE ALL CONSTRUCTION DEBRIS, EROSION CONTROL FENCING AND TRASH REMOVAL. THESE AREAS SHALL BE FINE GRADED AND SEEDED AND THE GRASSES ESTABLISHED PRIOR TO INITIAL ACCEPTANCE OF THE LANDSCAPING FOR THIS PROJECT.
- IN ALL LOCATIONS WHERE FIRE HYDRANTS WILL BE LOCATED, THERE SHALL BE A CLEAR AREA OF AT LEAST THREE FEET IN ALL DIRECTIONS AROUND EACH FIRE HYDRANT. THIS SHALL INCLUDE CLEARANCE FROM LANDSCAPING ITEMS SUCH AS BUSHES, SHRUBBERY, TREES, ETC., AS WELL AS PARKING SPACES, SIGNS, AND LIGHT POSTS, AND ANY OTHER POTENTIAL OBSTRUCTIONS.

MAINTENANCE NOTE

REFER TO CITY OF THORNTON SECTION 01000, PROJECT PROTECTION, MAINTENANCE & ACCEPTANCE GUIDELINES AND SPECIFICATIONS FOR COMPLETE INFORMATION REGARDING THIS SITE.

LANDSCAPE BASE BID NOTE

REFER TO THE SPECIFICATIONS FOR COMPLETE INFORMATION REGARDING ALL LANDSCAPE BASE BID ITEMS FOR THIS SITE.

ALLRED & ASSOCIATES

ARCHITECTURE | PLANNING | INTERIOR DESIGN

590 BURBANK ST. SUITE 125, BROOMFIELD, CO 80020 PHONE: 303.465.4392 FAX: 303.465.4392 www.allredarch.com

JOB NO. 24.100

BID SET

CITY OF THORNTON

FIRE STATION #8

15343 MONACO STREET

THORNTON, COLORADO 80602



REVISION NAME	DATE

ISSUE DATE: 2024 0927

meuran
designgroup
site design
landscape architecture
site planning

700 colorado boulevard, suite 131
denver, colorado 80206
303.512.0549 www.meuran.com

LANDSCAPE
NOTES & DETAILS

L1.3