



Sheet	Drawing Title
1	Cover Page
2	Site Plan
3	Lower Floor Plan
4	Upper Floor Plan
5	Elevations
6	Elevations
7	Lower Floor Coverings
8	Upper Floor Coverings
9	Electrical Lower Plan
10	Electrical Upper Plan
11	Health & Safety
12	Survey
13	Survey


Joanne Louise Redburn

BR250157

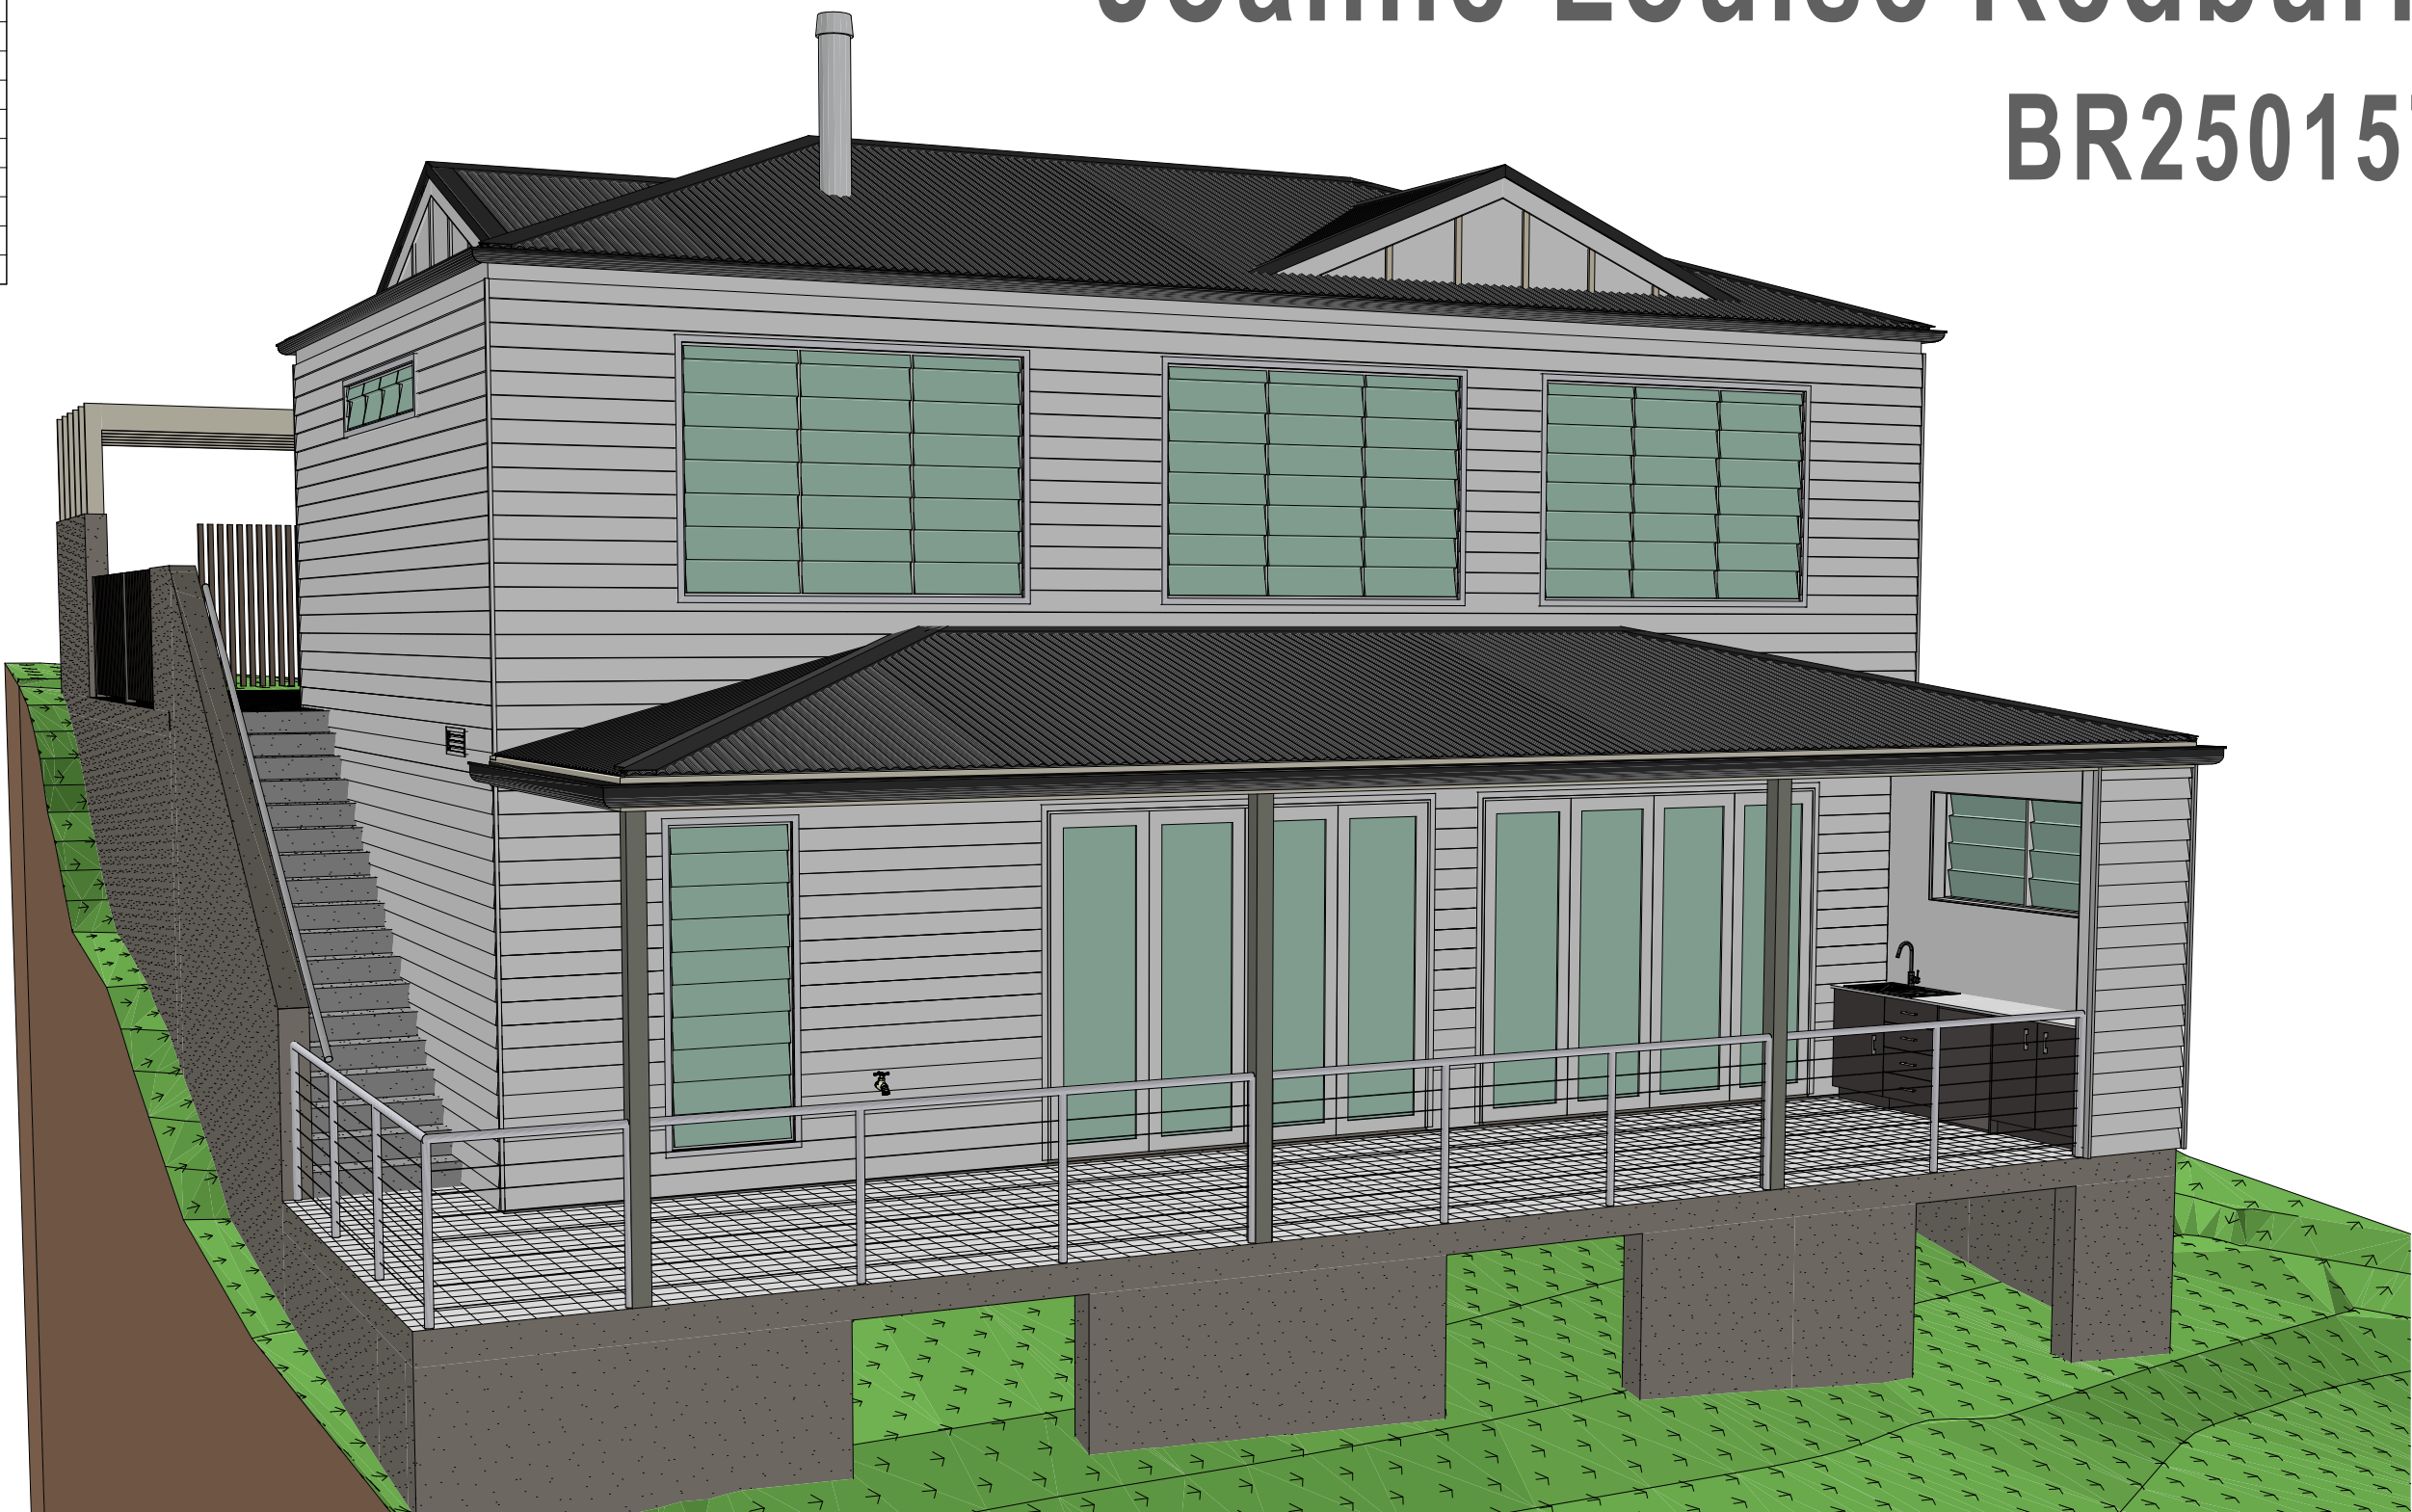

PERSPECTIVES ARE FOR ILLUSTRATION PURPOSES ONLY

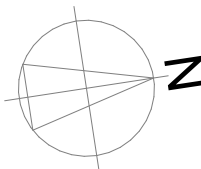
 INTEGRITY NEW HOMES	GENERAL NOTES: 1. Do not scale from drawings. 2. All dimensions to be checked on site. 3. Discrepancies to be reported to author. 4. Dimensions take precedence. 5. Boundaries to be verified by surveyor. 6. Other consultants drawings take precedence.			CLIENT NAMES: Joanne Louise Redburn			DESIGN TYPE: Design By Others		SITE CLASS: S-P		NORTH POINT: 	DRAWING TITLE: Cover Page		
	STREET No.: 76			LOT: 76	DP: SP245114	FACADE: Design By Others		WIND CLASS: N3		ISSUE: Prelim Council		AMENDMENT:	VERSION: 10	
	STREET ADDRESS: Annie Street, AUCHENFLOWER, QLD, 4066			LOCAL GOVERNMENT AUTHORITY: Brisbane City Council			DESIGNER: ER		ENVIRO. EXPOSURE CLASS: R1 Mild			SHEET: 1/13		DRAWING SCALE: NTS
	COPYRIGHT: These plans are copyright in whole & in part to InspireMeNow Pty Ltd & may not be used or reproduced without written permission			JOB NUMBER: BR250157			COLOUR SCHEME: N/A		BUSHFIRE CLASS: NIL			DRAWN BY: CM		DATE: 21/08/2026

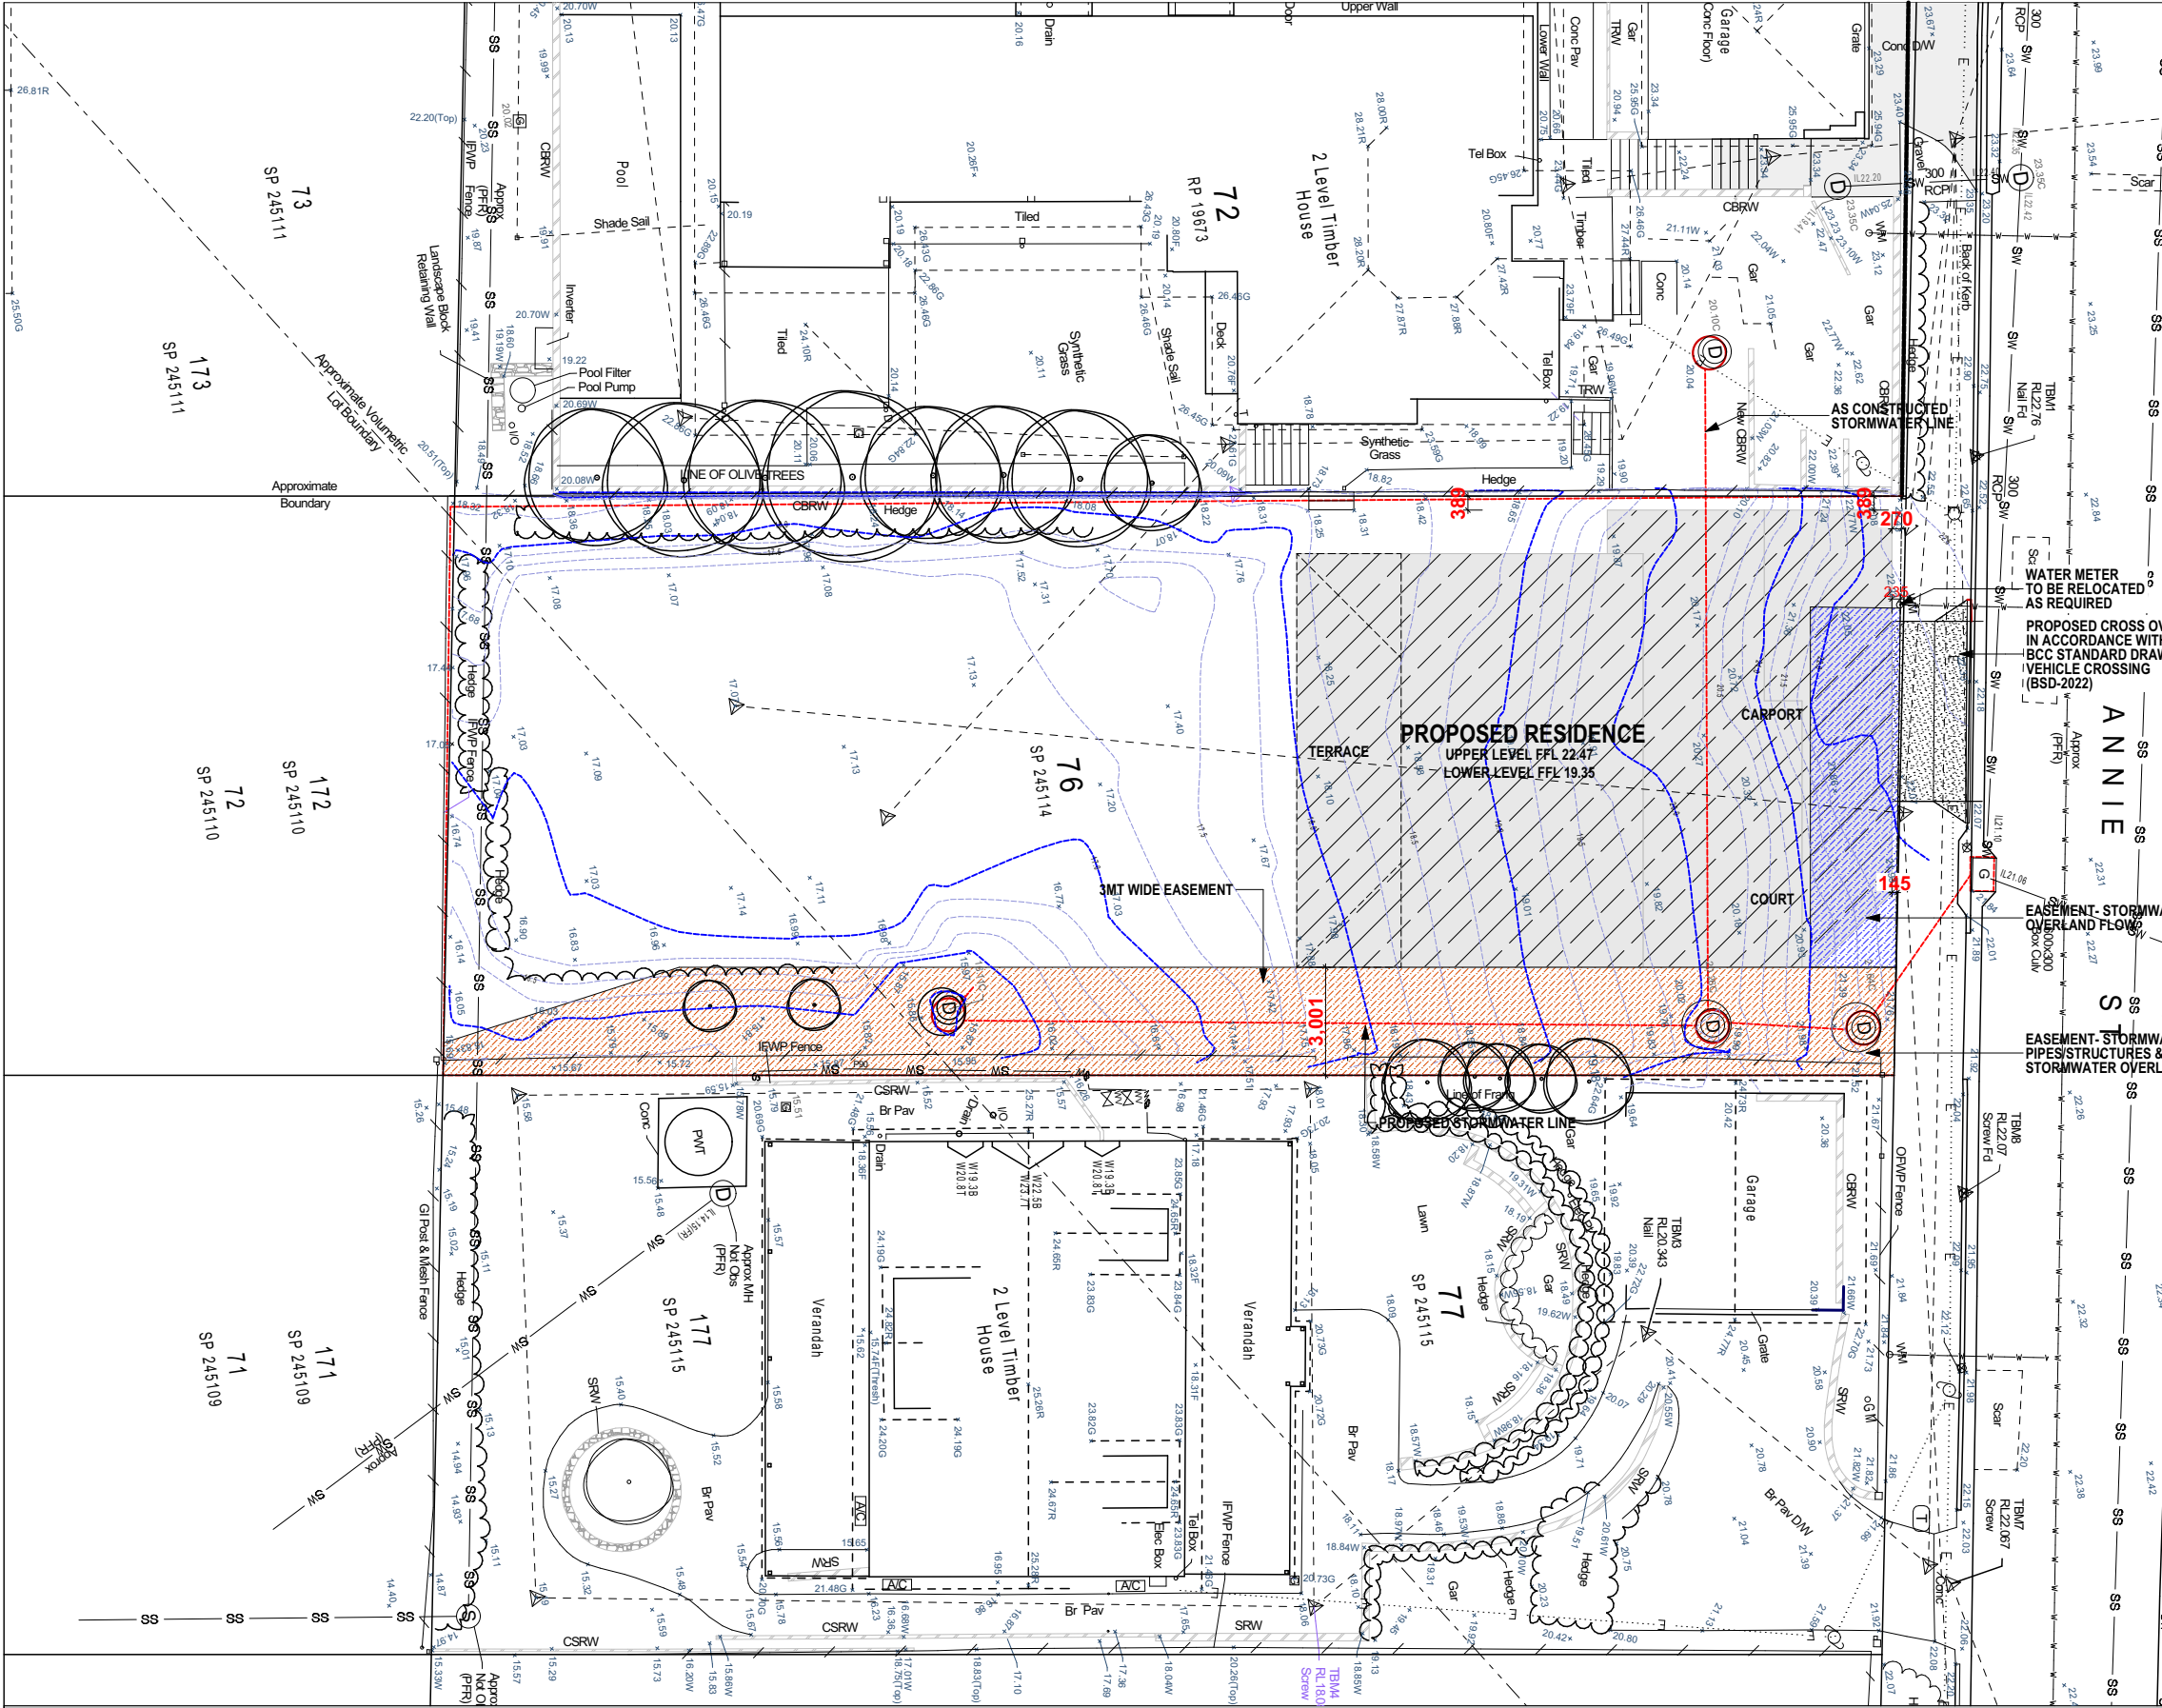

BUILDING LEVELS		
Project Zero R.L.: 22.25		
Level	R.L	Rise/Fall
Approx. Pad	22.25	+0mm
Approx. Sand Up	22.30	+50mm
Approx. Garage/Ext. Conc. FFL	22.53	+280mm
Approx. Living FFL	22.60	+350mm

ATTN: Rise and Fall is measured relative to Project Zero

LEGEND	
	Approximate Boundary
	Fence Line
	O/H Electric Wires
	Drainage (S/W) Pipe
	Sewer Pipe
	Water Pipe
	Approx Volumetric Lot Bdy
	MH Cover Level
	Floor Level
	Top of Guttering Level
	Roof Ridge Level
	Top of Wall Level
	Boundary Monument Fd
	Conc Block Retaining Wall
	Conc Sleeper Retaining Wall
	Stone Retaining Wall
	Timber Retaining Wall
	Downpipe
	Drainage Grate
	Electric Pole
	Fire Hydrant
	Gas Meter
	Inside Face Wood Paling
	Lamp Post
	From Records
	Plotted From Records
	Sewer Manhole
	Sewer Inspection Opening
	Level Observation
	Survey Traverse/ Benchmark
	Telecom Pit
	Tree (Plotted to Scale)
	Water Meter
	Water Tap
	Water Valve





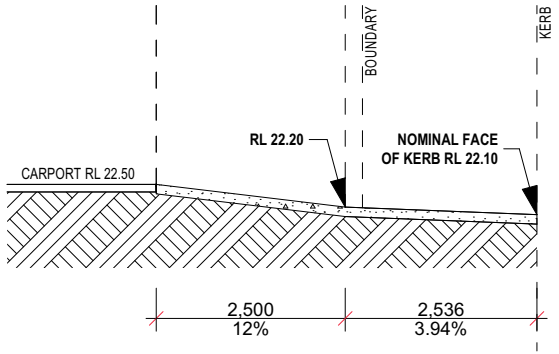


DRIVEWAY GRADIENT

	GENERAL NOTES: 1. Do not scale from drawings. 2. All dimensions to be checked on site. 3. Discrepancies to be reported to author. 4. Dimensions take precedence. 5. Boundaries to be verified by surveyor. 6. Other consultants drawings take precedence.			CLIENT NAMES: Joanne Louise Redburn		DESIGN TYPE: Design By Others		SITE CLASS: S-P		NORTH POINT:		DRAWING TITLE: Site Plan	
	COPYRIGHT: These plans are copyright in whole & in part to InspireMeNow Pty Ltd & may not be used or reproduced without written permission			STREET No.: 76		LOT: 76		DP: SP245114		WIND CLASS: N3		ISSUE: Prelim Council	
	STREET ADDRESS: Annie Street, AUCHENFLOWER, QLD, 4066			LOCAL GOVERNMENT AUTHORITY: Brisbane City Council		DESIGNER: ER		ENVIRO. EXPOSURE CLASS: R1 Mild		SHEET: 2/13		DRAWING SCALE: 1:200, 1:100	
	JOB NUMBER: BR250157			COLOUR SCHEME: N/A		BUSHFIRE CLASS: NIL		DRAWN BY: CM		DATE: 21/08/2026			

Areas	
1. Lower Living	77.33
2. Upper Living	76.41
3. Storage	51.65
4. Carport	42.08
5. Terrace	33.32
	280.79 m ²

Lower Ext Perimeter:	36.44 l/m
(inc 18.02 l/m of cladding)	
Upper Ext Perimeter:	36.28 l/m
Wet Areas:	19.15m ²

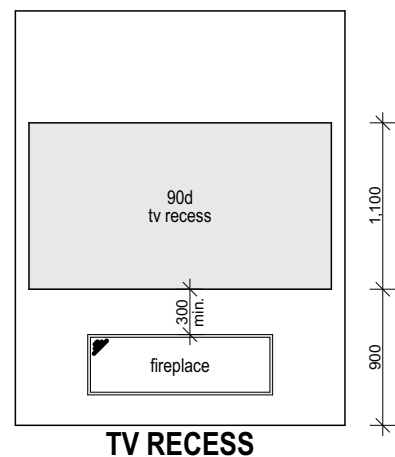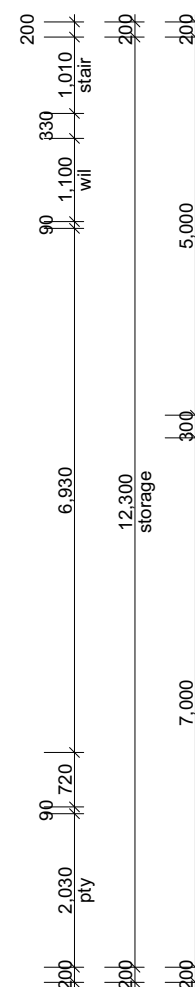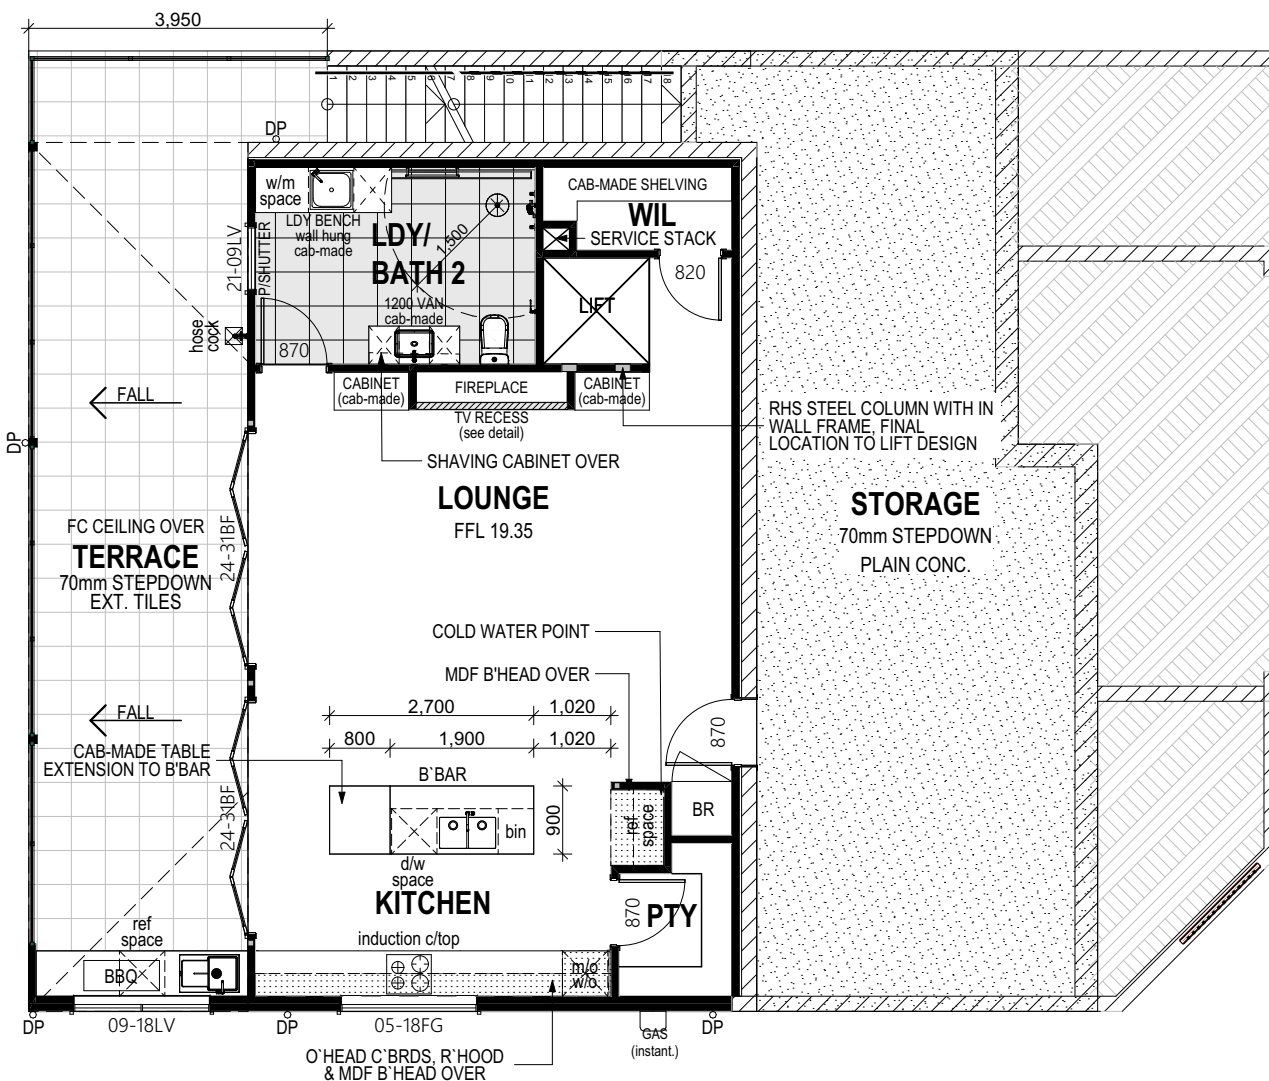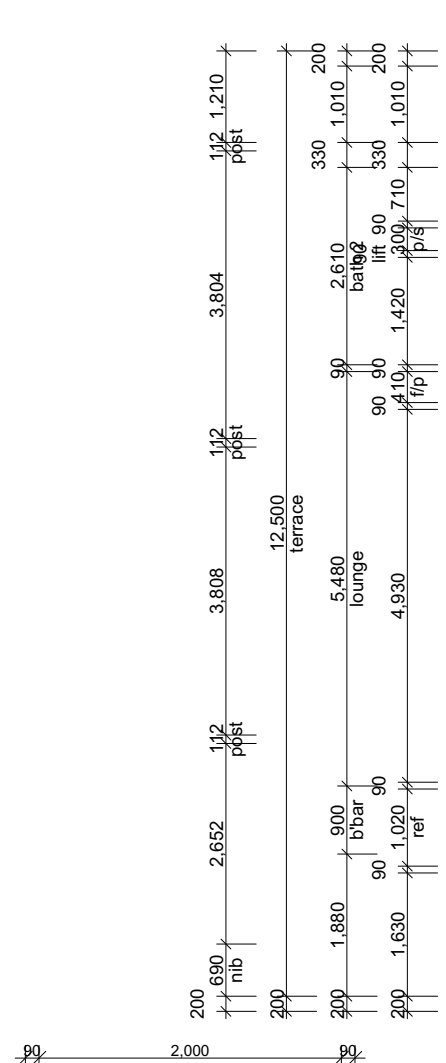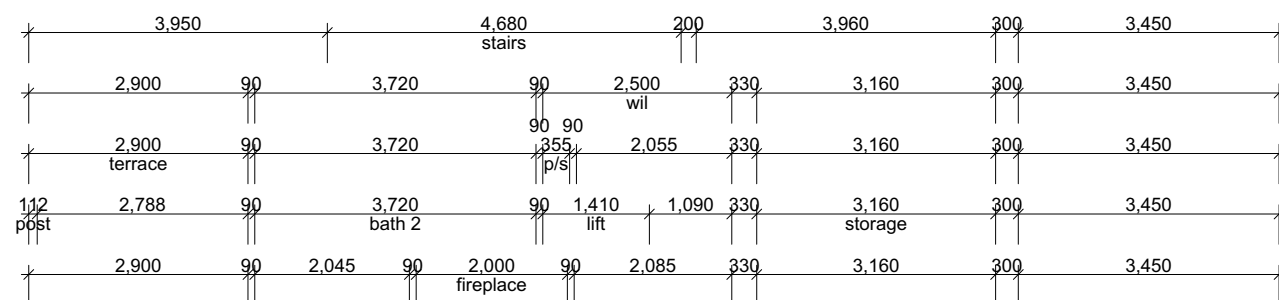

NOTE:
FINAL LAYOUTS MAY REQUIRE BULKHEADS AND SERVICE
STACKS PENDING COMPLETED SERVICE DESIGNS

NOTE:
CEILING HEIGHT WALL TILES TO BATH 1 & LDY/BATH 2

NOTE:
GREY GLAZING THROUGHOUT EXCL. BATH 1 & LDY/BATH 2

NOTE:
2340h INTERNAL DOORS THROUGHOUT

NOTE:
SQ-SET CEILING THROUGHOUT



CLIENT NAMES:
Joanne Louise Redburn

STREET No.: LOT: DP:
76 76 SP245114

SITE ADDRESS:
Annie Street, AUCHENFLOWER, QLD, 4066

LOCAL GOVERNMENT AUTHORITY:
Brisbane City Council

DESIGN TYPE: Design By Others	JOB NUMBER: BR250157
----------------------------------	-------------------------

FACADE: Design By Others	DESIGNER: ER
-----------------------------	-----------------

COLOUR SCHEME:
N/A


ENVIRO. EXPOSURE CLASS: R1 Mild	SITE CLASS: S-P
---	---------------------------

BUSHFIRE CLASS:	WIND CLASS:
NIL	N3

GENERAL NOTES:

1. Do not scale from drawings.
2. All dimensions to be checked on site.
3. Discrepancies to be reported to author.
4. Dimensions take precedence.
5. Boundaries to be verified by surveyor.
6. Other consultants drawings take precedence.

NORTH POINT:

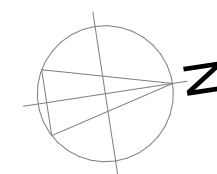



DRAWING TITLE:
Lower Floor Plan

ISSUE: Prelim Council	AMENDMENT:	VERSION: 10
--------------------------	------------	----------------

SHEET: 3/13	DRAWING SCALE 1:100, 1:1
----------------	-----------------------------

DRAWN BY: CM	DATE: 21/08/2026
-----------------	---------------------

COPYRIGHT:
These plans are copyright in whole & in part to InspireMeNow Pty Ltd & may not be used or reproduced without written permission

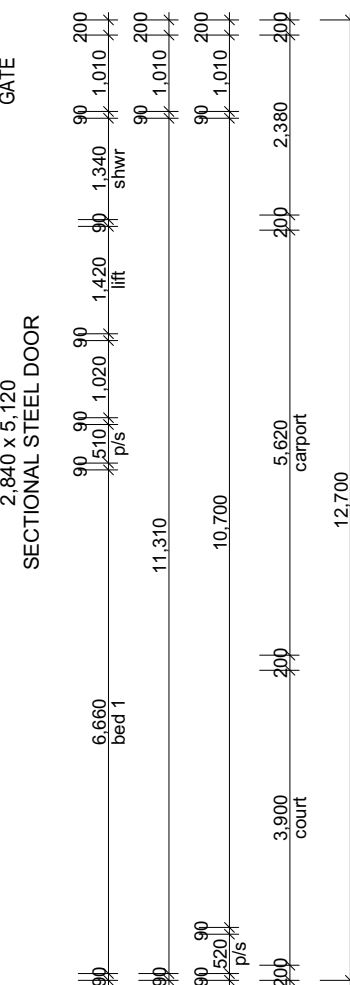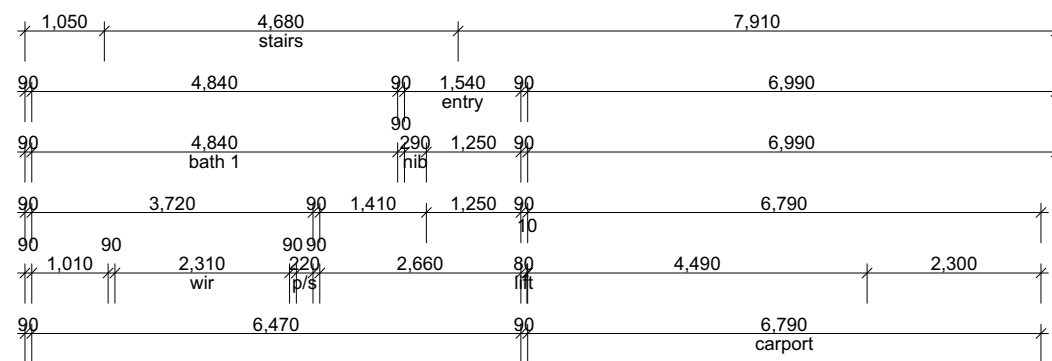[illegible]

Wall Type	Cross Section
200mm CSR Rediwall	
200mm Ext. Wall w/ Plaster 1 Side	
300mm CSR Rediwall	
330mm CRS Rediwall/ 90mm Int. wall	
90mm Ext. Wall (No Plaster)	
90mm Ext. Wall w/ Plaster 1 Side	
90mm Int. Wall Low Wall w/ Plaster Both Sides	
90mm Int. Wall w/ Plaster 1 Side	
90mm Int. Wall w/ Plaster Both Sides	


NOTE:
SQ-SET CEILING THROUGHOUT



BUSHFIRE CLASS: NIL	WIND CLASS: N3
------------------------	-------------------


GENERAL NOTES:

1. Do not scale from drawings.
2. All dimensions to be checked on site.
3. Discrepancies to be reported to author.
4. Dimensions take precedence.
5. Boundaries to be verified by surveyor.
6. Other consultants drawings take precedence.

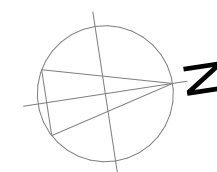


COPYRIGHT:
These plans are copyright in whole & in part to InspireMeNow Pty Ltd & may not be used or reproduced without written permission

NOTE:
THESE DRAWINGS ARE A PICTORIAL INDICATION ONLY,
SOME VARIATION MAY OCCUR ON SITE.

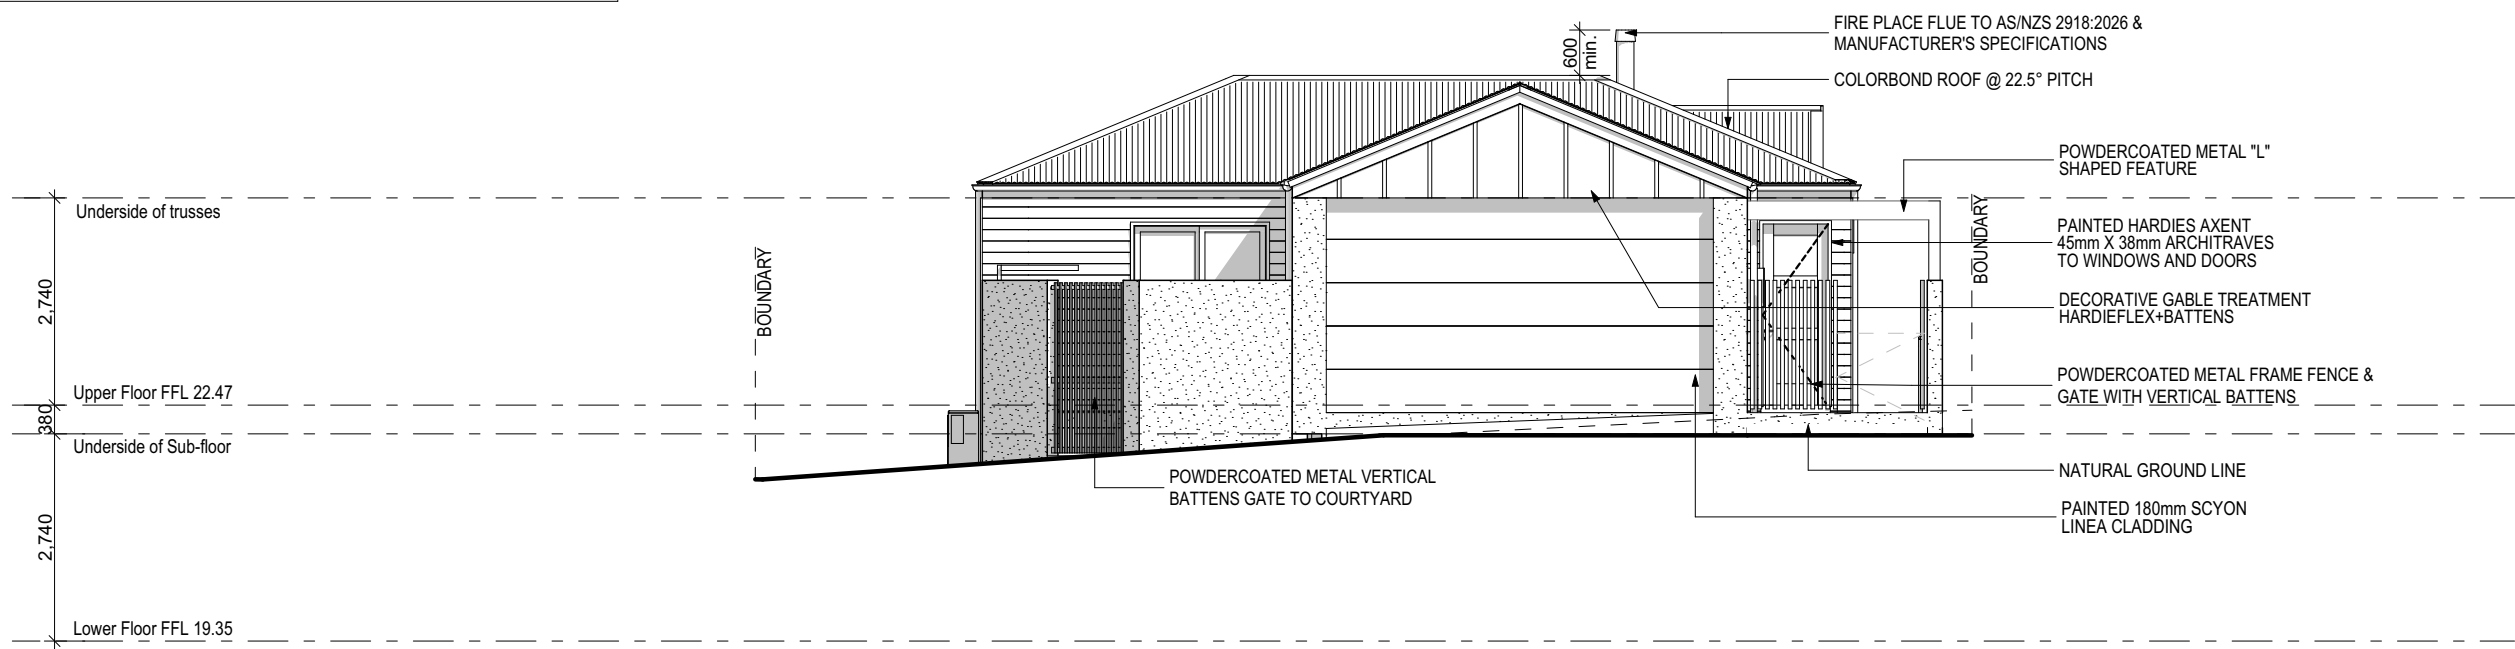

Front Elevation - North Facing

**AJ = ARTICULATION JOINT
TO ENGINEERS DETAIL**

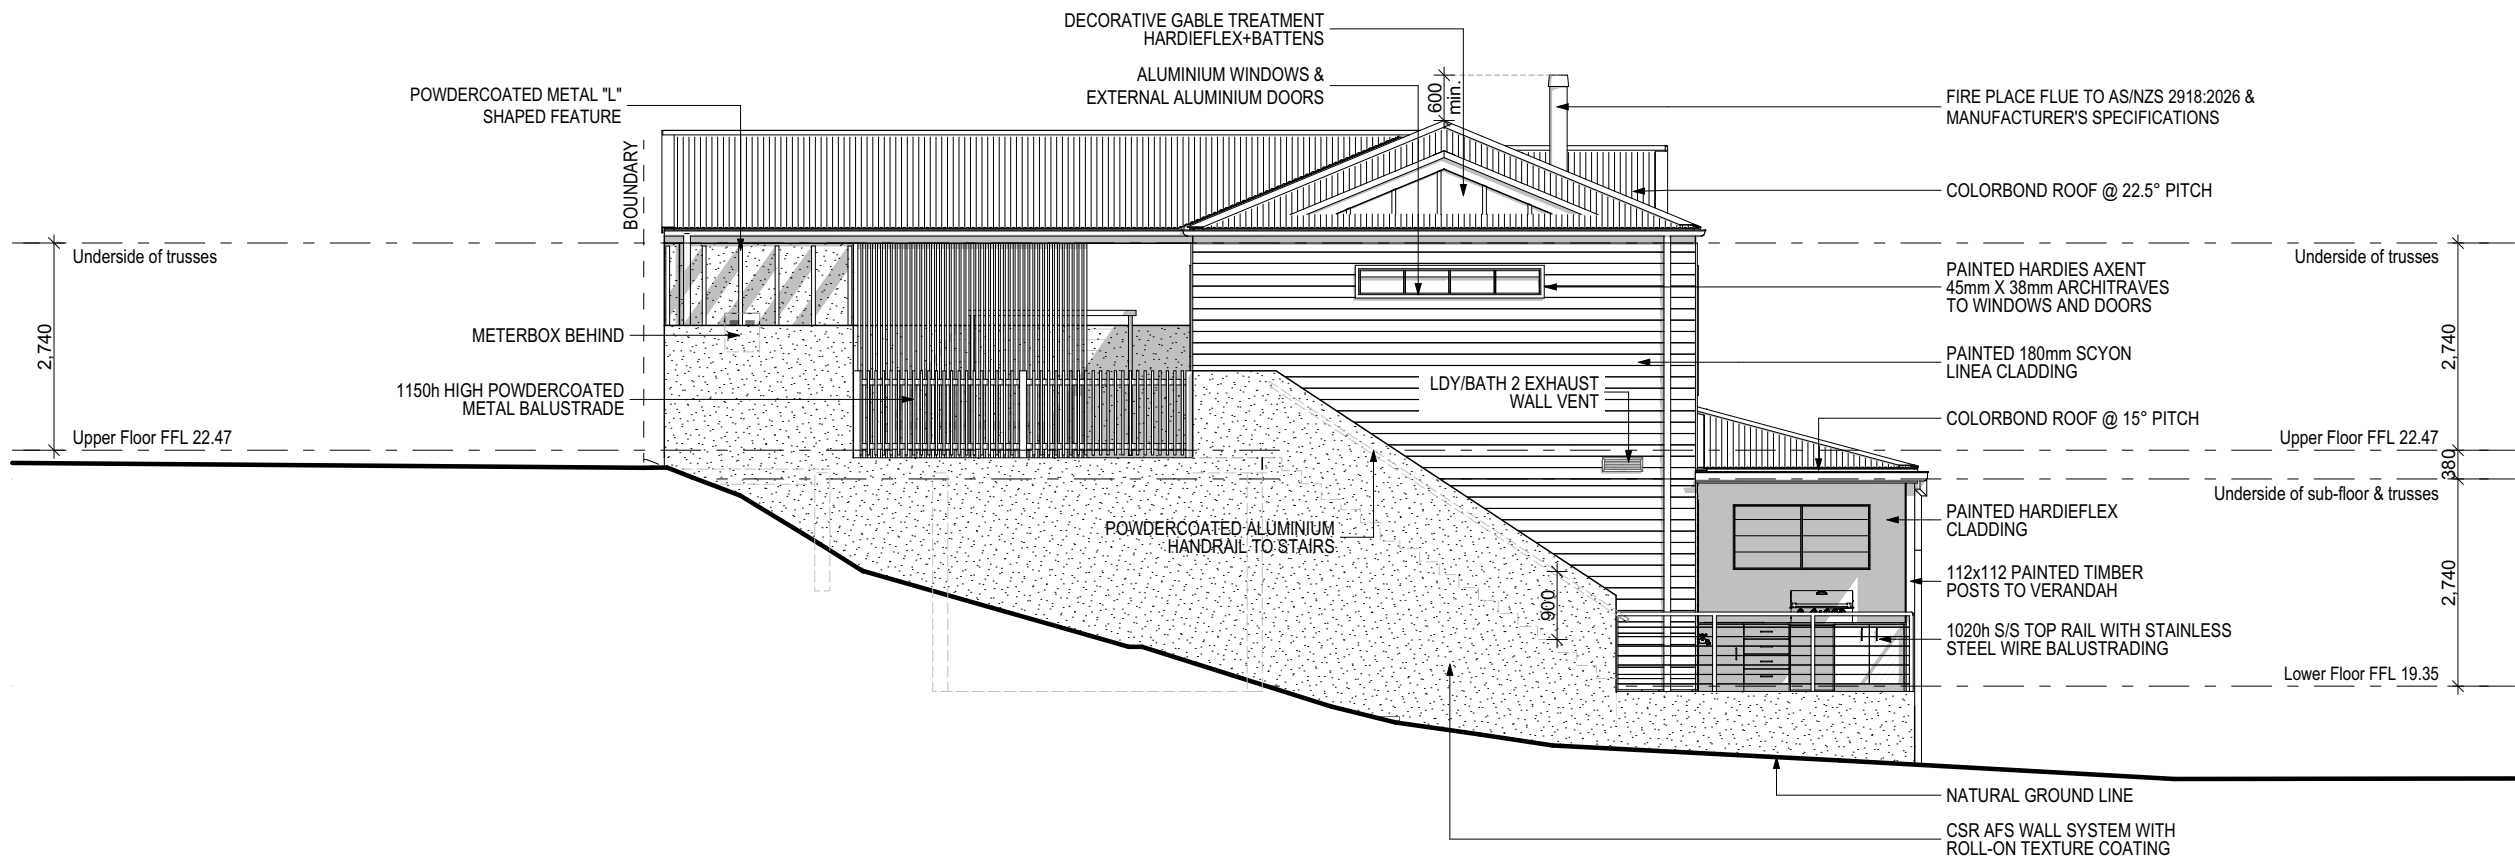

Right Elevation - West Facing



CLIENT NAMES:
Joanne Louise Redburn

STREET No.: 76 LOT: 76 DP: SP245114

SITE ADDRESS:
Annie Street, AUCHENFLOWER, QLD, 4066

LOCAL GOVERNMENT AUTHORITY:
Brisbane City Council

DESIGN TYPE: Design By Others JOB NUMBER: BR250157


FACADE: Design By Others DESIGNER: ER

COLOUR SCHEME:
N/A

ENVIRO. EXPOSURE CLASS: R1 Mild SITE CLASS: S-P

BUSHFIRE CLASS: NIL WIND CLASS: N3

GENERAL NOTES:
1. Do not scale from drawings.
2. All dimensions to be checked on site.
3. Discrepancies to be reported to author.
4. Dimensions take precedence.
5. Boundaries to be verified by surveyor.
6. Other consultants drawings take precedence.

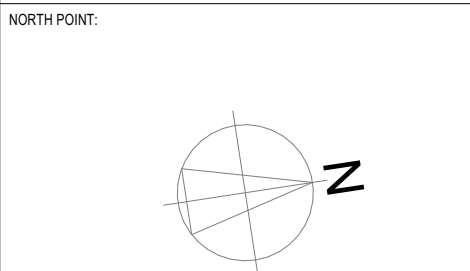

DRAWING TITLE:
Elevations


ISSUE: Prelim Council AMENDMENT: VERSION: 10

SHEET: 5/13 DRAWING SCALE: 1:100

DRAWN BY: CM DATE: 21/08/2026


COPYRIGHT:
These plans are copyright in whole & in part to InspireMeNow Pty Ltd & may not be used or reproduced without written permission

NOTE:
THESE DRAWINGS ARE A PICTORIAL INDICATION ONLY,
SOME VARIATION MAY OCCUR ON SITE.

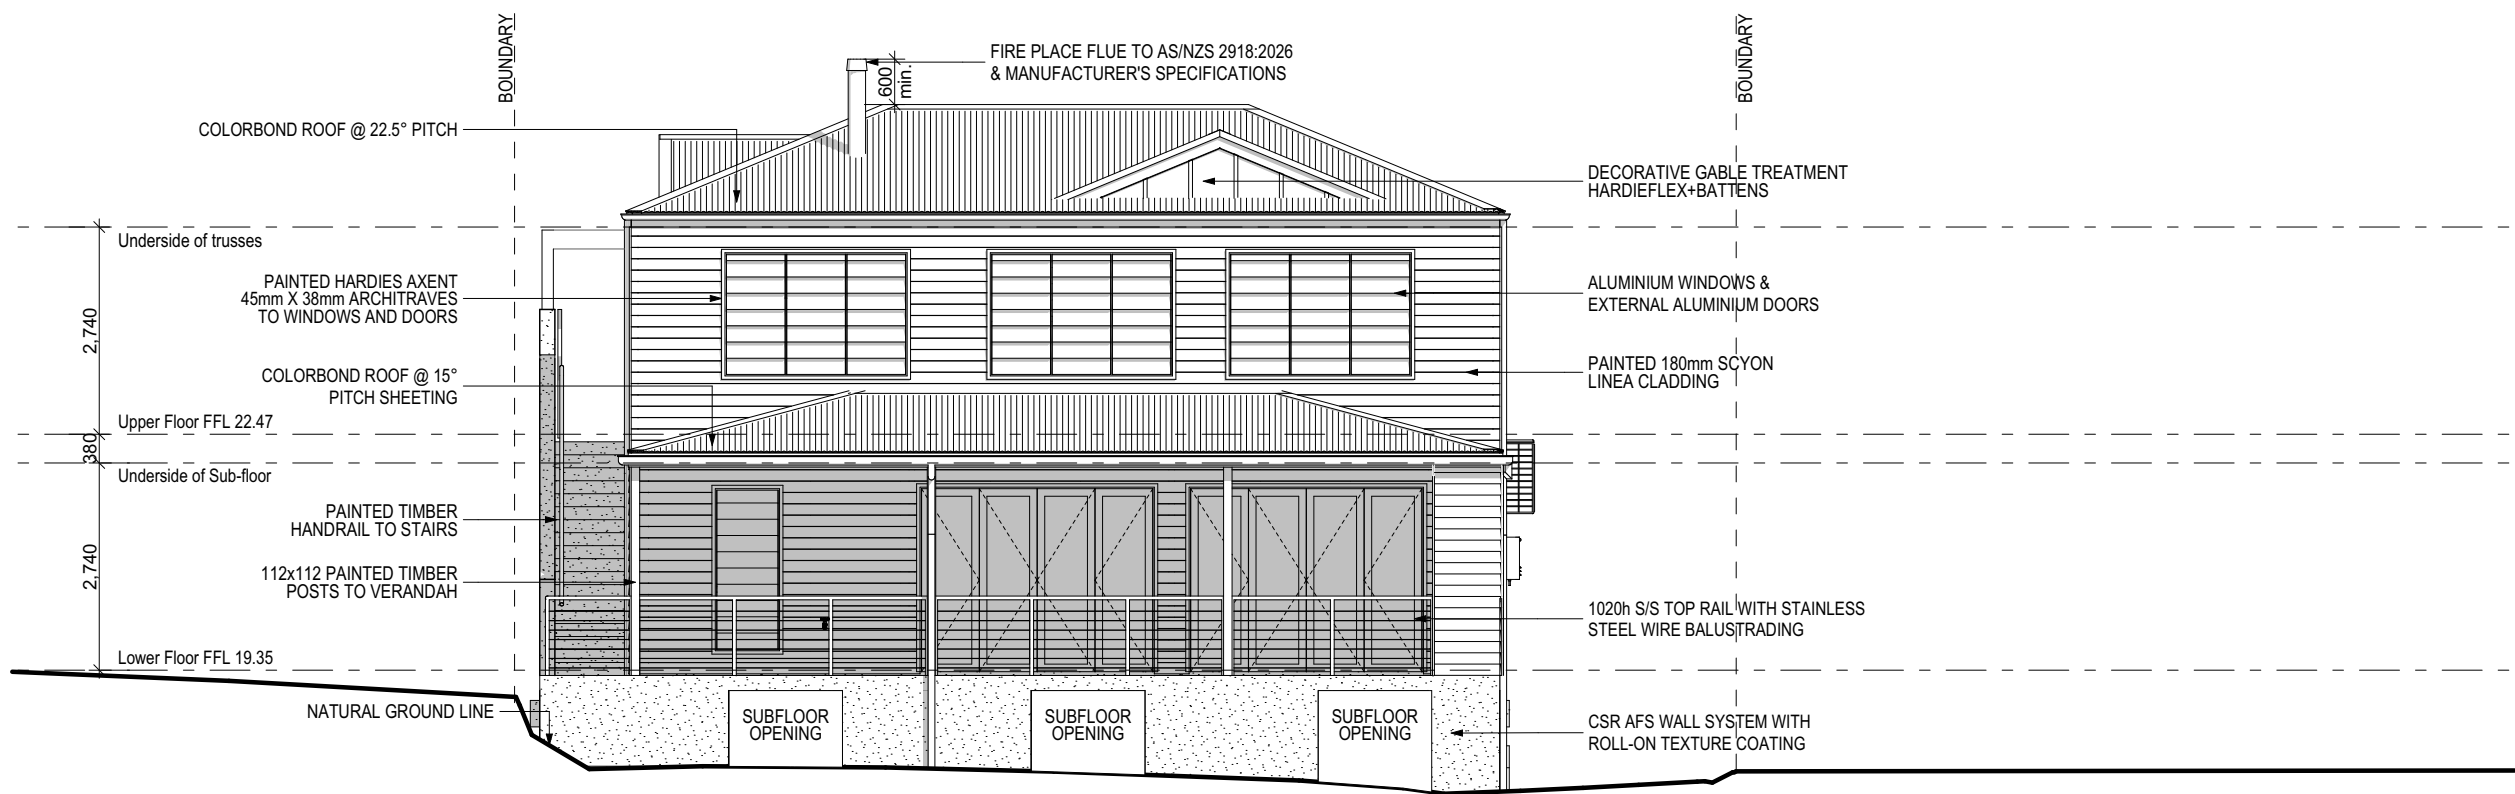

Rear Elevation - South Facing

**AJ = ARTICULATION JOINT
TO ENGINEERS DETAIL**

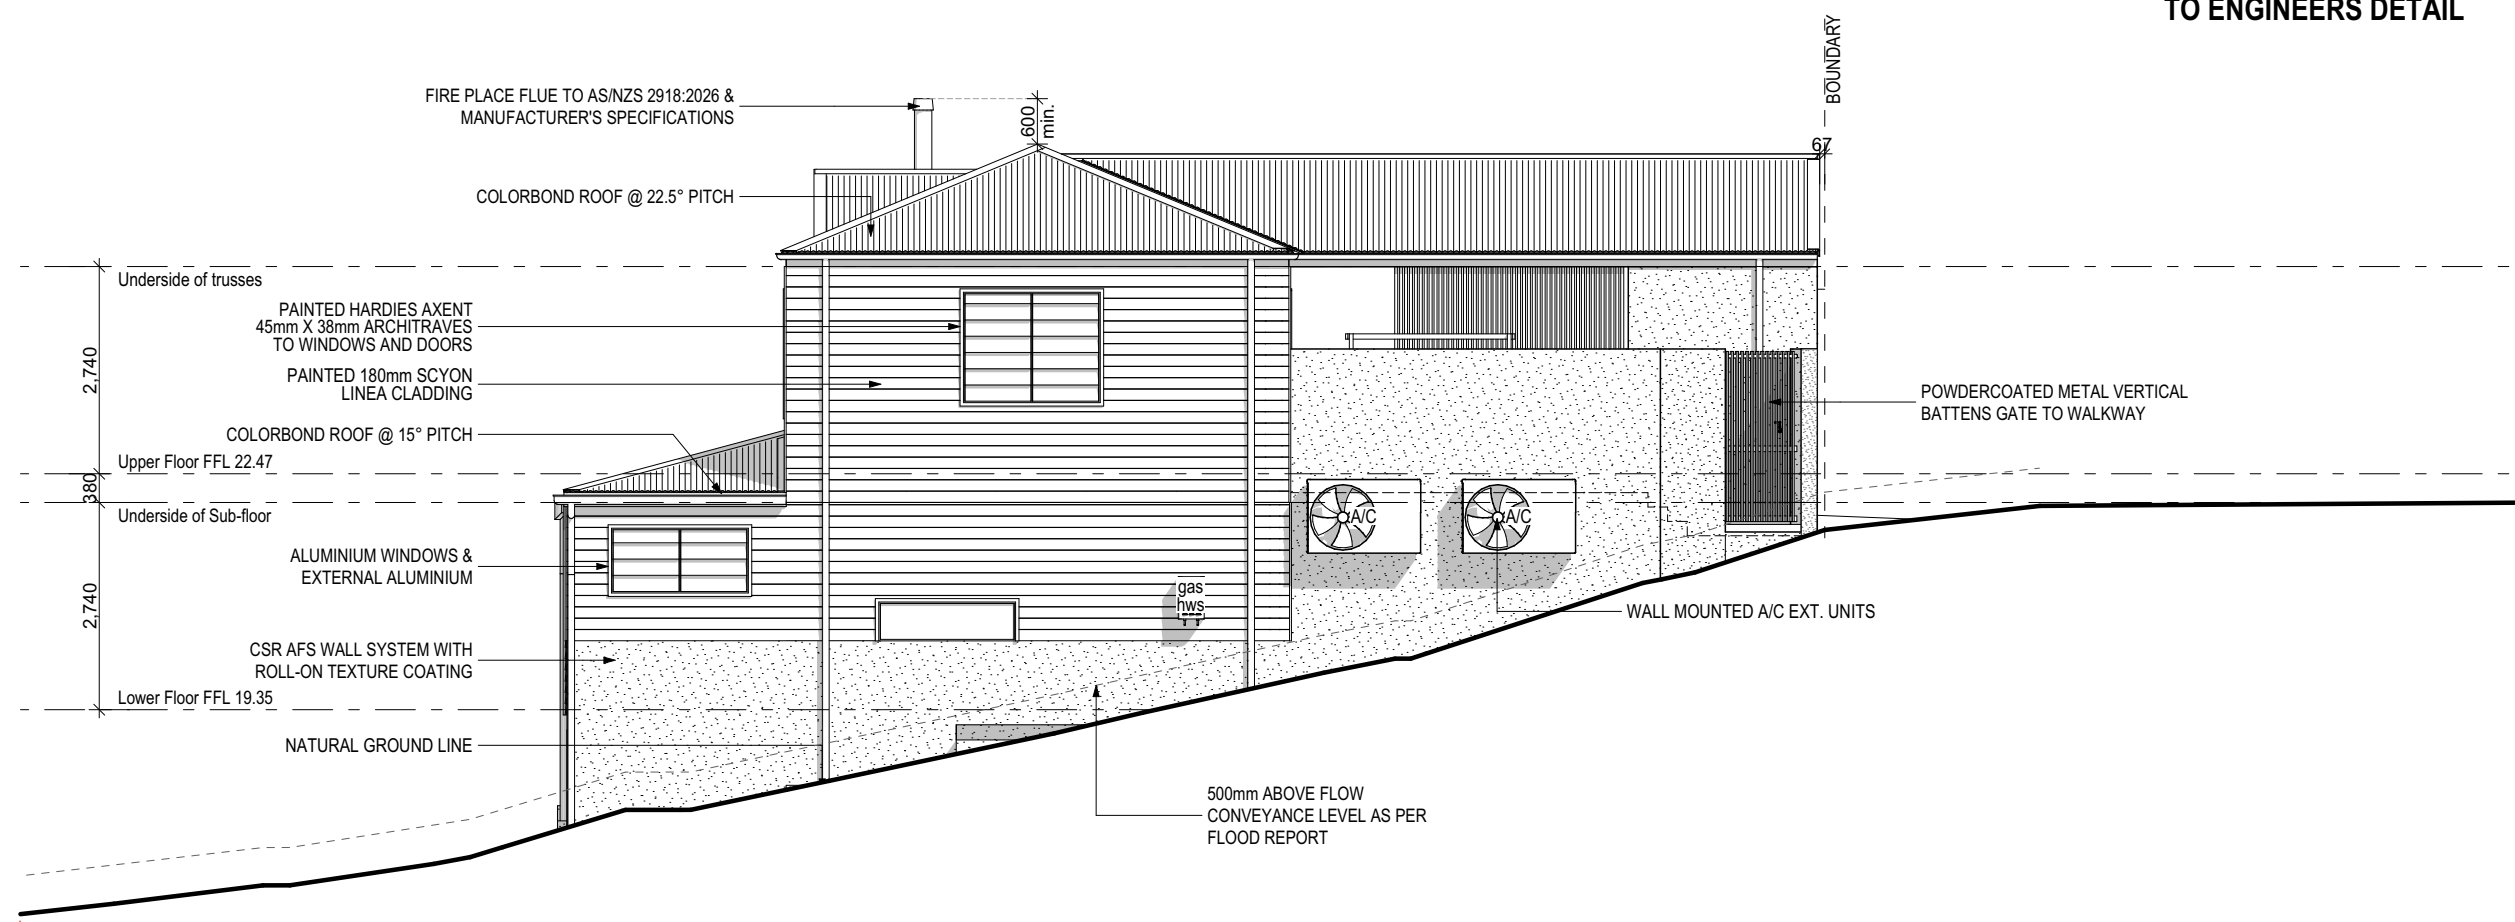


Left Elevation - East Facing



CLIENT NAMES: Joanne Louise Redburn		
STREET No.: 76	LOT: 76	DP: SP245114
SITE ADDRESS: Annie Street, AUCHENFLOWER, QLD, 4066		
LOCAL GOVERNMENT AUTHORITY: Brisbane City Council		
DESIGN TYPE: Design By Others		JOB NUMBER: BR250157
FACADE: Design By Others	DESIGNER: ER	
COLOUR SCHEME: N/A		
ENVIRO. EXPOSURE CLASS: R1 Mild	SITE CLASS: S-P	
BUSHFIRE CLASS: NIL	WIND CLASS: N3	

GENERAL NOTES:
1. Do not scale from drawings.
2. All dimensions to be checked on site.
3. Discrepancies to be reported to author.
4. Dimensions take precedence.
5. Boundaries to be verified by surveyor.
6. Other consultants drawings take precedence.

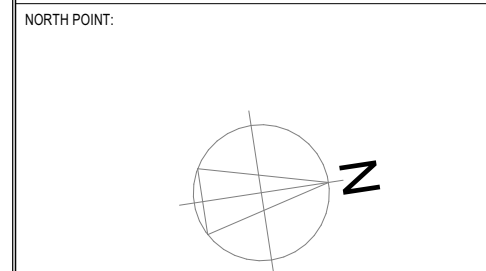


DRAWING TITLE: Elevations		
ISSUE: Prelim Council	AMENDMENT:	VERSION: 10
SHEET: 6/13	DRAWING SCALE: 1:100	
DRAWN BY: CM	DATE: 21/08/2026	


COPYRIGHT:
These plans are copyright in whole & in part to InspireMeNow
Pty Ltd & may not be used or reproduced without written
permission


Lower Floor Coverings Approx. Areas (not inc. waste)		
Type	Area	Fill
Ext. Tiles	36.13	
Ext. Tiles (stair treads/risers)	7.85	
Hybrid Flooring	51.21	
Wet Area Tiles	10.10	

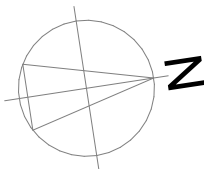

	GENERAL NOTES: 1. Do not scale from drawings. 2. All dimensions to be checked on site. 3. Discrepancies to be reported to author. 4. Dimensions take precedence. 5. Boundaries to be verified by surveyor. 6. Other consultants drawings take precedence. COPYRIGHT: These plans are copyright in whole & in part to InspireMeNow Pty Ltd & may not be used or reproduced without written permission	CLIENT NAMES: Joanne Louise Redburn			DESIGN TYPE: Design By Others	SITE CLASS: S-P	NORTH POINT: 	DRAWING TITLE: Lower Floor Coverings				
		STREET No.: 76			LOT: 76	DP: SP245114		FACADE: Design By Others	WIND CLASS: N3	ISSUE: Prelim Council	AMENDMENT:	VERSION: 10
		STREET ADDRESS: Annie Street, AUCHENFLOWER, QLD, 4066			DESIGNER: ER	ENVIRO. EXPOSURE CLASS: R1 Mild		SHEET: 7/13		DRAWING SCALE: 1:100		
		LOCAL GOVERNMENT AUTHORITY: Brisbane City Council			COLOUR SCHEME: N/A	BUSHFIRE CLASS: NIL		DRAWN BY: CM		DATE: 21/08/2026		

Upper Floor Coverings Approx. Areas (not inc. waste)		
Type	Area	Fill
Ext. Tiles	18.46	
T & G Timber	59.46	
Wet Area Tiles	9.18	

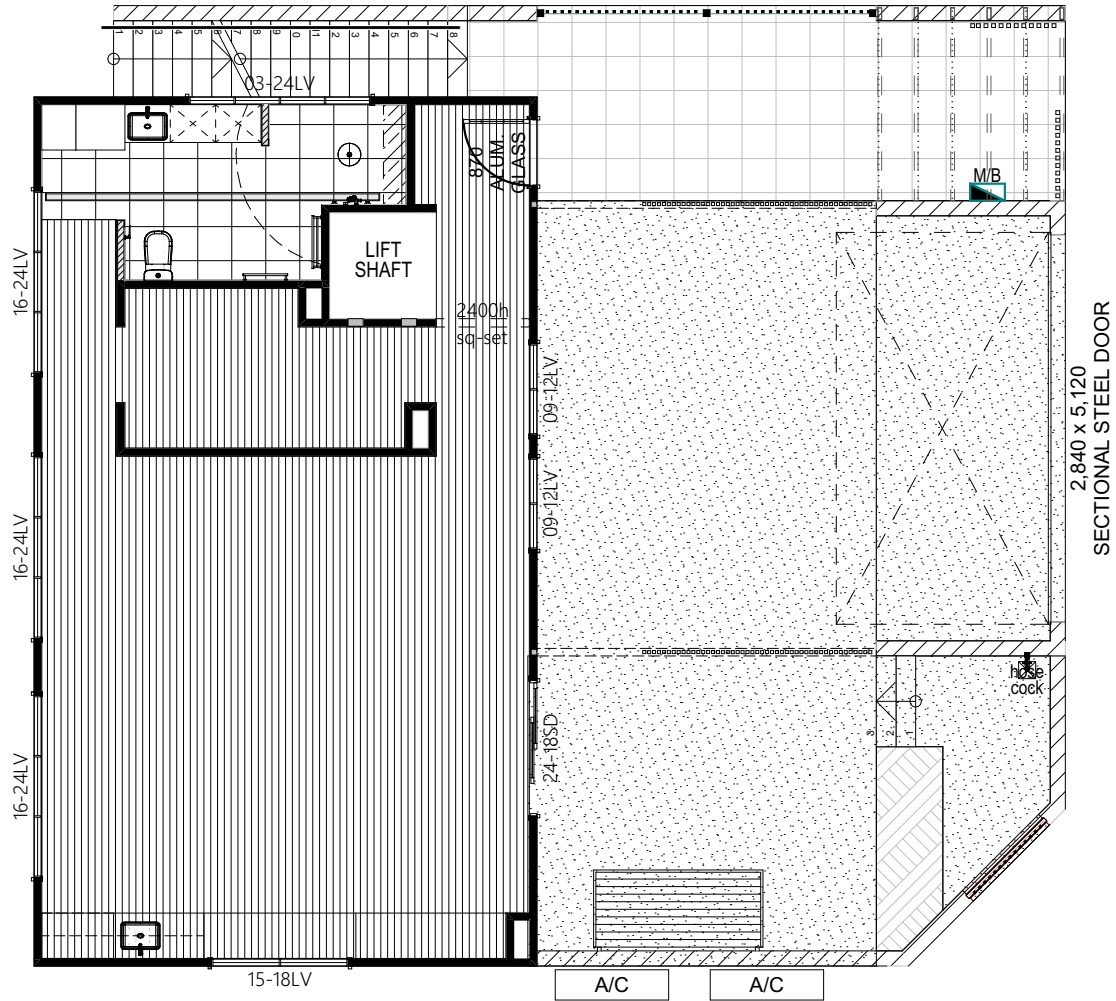

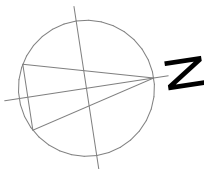	GENERAL NOTES: 1. Do not scale from drawings. 2. All dimensions to be checked on site. 3. Discrepancies to be reported to author. 4. Dimensions take precedence. 5. Boundaries to be verified by surveyor. 6. Other consultants drawings take precedence. COPYRIGHT: These plans are copyright in whole & in part to InspireMeNow Pty Ltd & may not be used or reproduced without written permission	CLIENT NAMES: Joanne Louise Redburn		DESIGN TYPE: Design By Others	SITE CLASS: S-P	NORTH POINT: 	DRAWING TITLE: Upper Floor Coverings				
		STREET No.: 76		LOT: 76	DP: SP245114		FACADE: Design By Others	WIND CLASS: N3	ISSUE: Prelim Council	AMENDMENT:	VERSION: 10
		STREET ADDRESS: Annie Street, AUCHENFLOWER, QLD, 4066			DESIGNER: ER		ENVIRO. EXPOSURE CLASS: R1 Mild	SHEET: 8/13		DRAWING SCALE: 1:100	
		LOCAL GOVERNMENT AUTHORITY: Brisbane City Council			COLOUR SCHEME: N/A		BUSHFIRE CLASS: NIL	DRAWN BY: CM		DATE: 21/08/2026	

STANDARD ELECTRICAL HEIGHTS

GPO'S

-ALL GPO'S NOT LISTED BELOW ARE TO BE 300mm AFL (UNO)

-KITCHEN BENCH	1050mm
-BREAKFAST BAR (B'BAR)	750mm
-RANGE HOOD (R'HOOD)	1900mm
-MICROWAVE (m/o)	750mm
-REFRIGERATOR (REF)	1900mm
-DISHWASHER (d/w)	300mm
-WASHING MACHINE (w/m)	1050mm
-LAUNDRY BENCH	1050mm
-VANITIES	1050mm


INTERNAL/ EXTERNAL LIGHTS

- LIGHT SWITCHES ARE TO BE INSTALLED AT 1300mm AFL (UNO)
- WALL MOUNTED LIGHTS ARE TO BE INSTALLED AT 2000mm AFL (UNO)

CONNECTIVITY

- TV POINTS ARE TO BE INSTALLED AT 400mm AFL DIRECTLY ABOVE THE CLOSEST GPO (UNO)
- PHONE POINTS ARE TO BE INSTALLED AT 1150mm AFL DIRECTLY ABOVE THE CLOSEST GPO (UNO)
- DATA POINTS ARE TO BE INSTALLED AT 400mm AFL DIRECTLY ABOVE THE CLOSEST GPO (UNO)

(HEIGHTS SPECIFIED ARE TO THE CENTRE LINE OF THE ELECTRICAL FIXTURE)

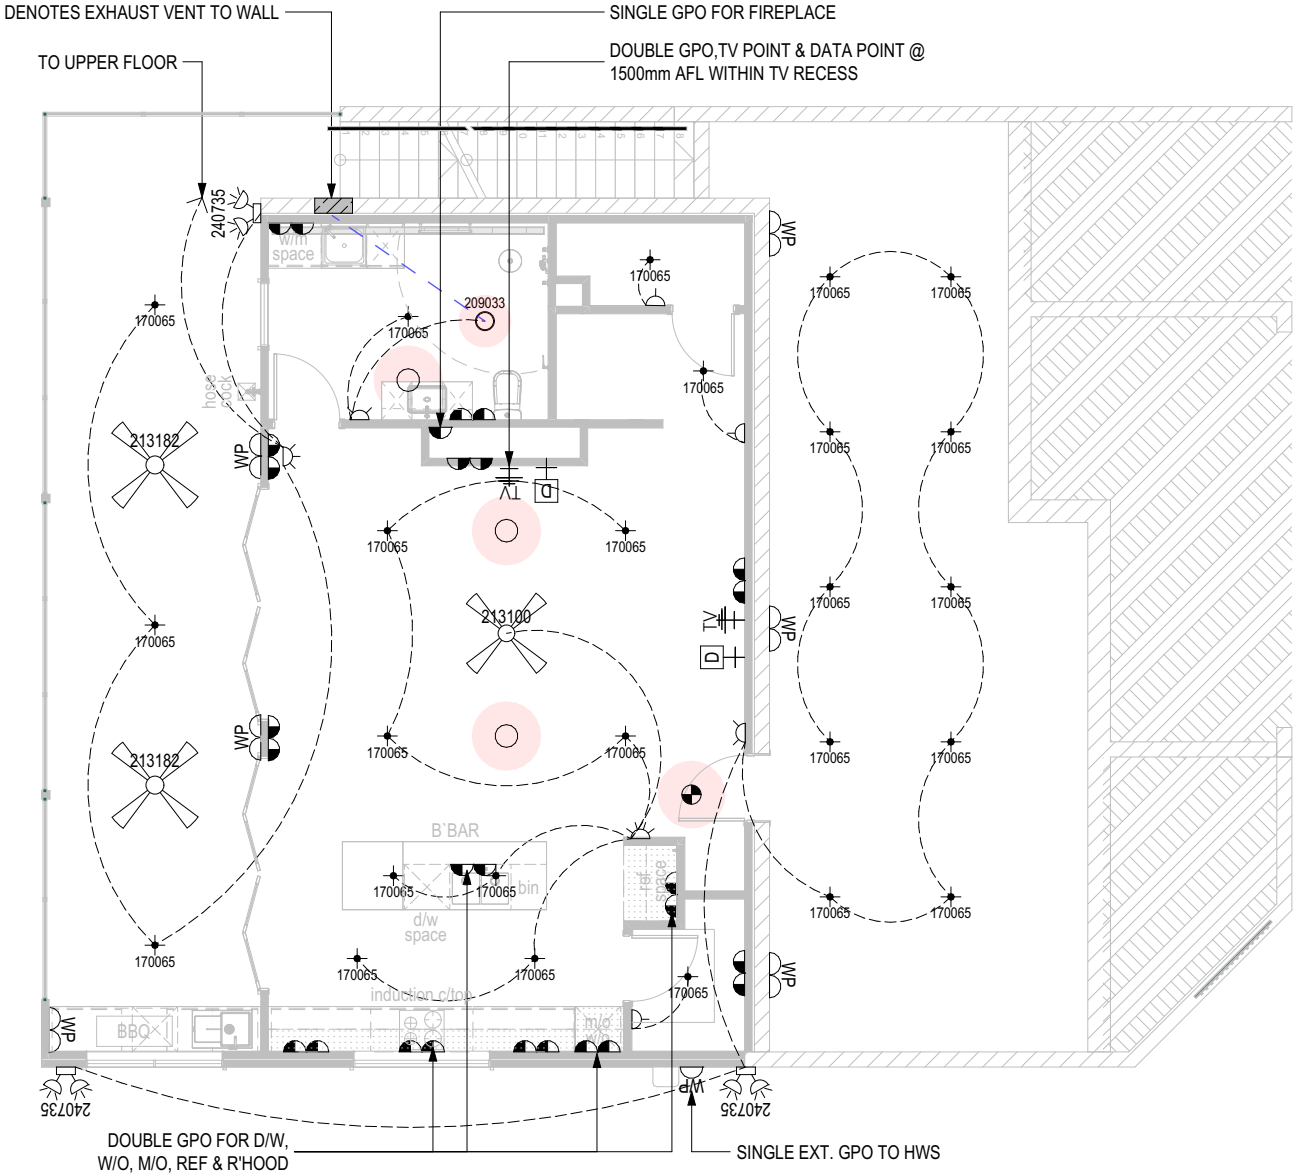

Electrical		
Electrical Item	Symbol	Quantity
170065 - Eclipse Maxi LED Colour Switch DL - White	170065	35
189302 - 1200mm LED Batten - White	189302	4
209033 - Reef 200mm Round Exhaust Fan - White	209033	2
213100 - Aria 132cm Fan with Wall Control - White	213100	2
213182 - Atlanta 142cm Fan and Light with Remote - White	213182	2
221125 - Sunset Illumo Solar LED Sensor Wall Light - Black	221125	4
239662 - Wanaka 2 Light Adjustable Wall Light - White	239662	3
240735 - Sentinel 2 Light Spotlight with Sensor - Black	240735	7
AC Vent - Round		6
Datapoint		3
Double GPO		20
Double GPO Weather Proof		7
Exhaust Vent		1
Garage Remote	Remote	1
Light Switch - Double		4
Light Switch - Four		2
Light Switch - Single		5
Light Switch - Triple		2
Sensor		1
Single GPO		2
Single GPO Weather Proof		1
Smoke Alarm		2
TV Point		3
Weather Proof Isolator Switch - Air Conditioning		2



GENERAL NOTES:

1. Do not scale from drawings.
2. All dimensions to be checked on site.
3. Discrepancies to be reported to author.
4. Dimensions take precedence.
5. Boundaries to be verified by surveyor.
6. Other consultants drawings take precedence.

COPYRIGHT:

These plans are copyright in whole & in part to InspireMeNow Pty Ltd & may not be used or reproduced without written permission

CLIENT NAMES:

Joanne Louise Redburn

STREET No.:

76

LOT:

76

DP:

SP245114

STREET ADDRESS:

Annie Street, AUCHENFLOWER, QLD, 4066

LOCAL GOVERNMENT AUTHORITY:

Brisbane City Council

JOB NUMBER:

BR250157

DESIGN TYPE:

Design By Others

FACADE:

Design By Others

DESIGNER:

ER

COLOUR SCHEME:

N/A

SITE CLASS:

S-P

WIND CLASS:

N3


ENVIRO. EXPOSURE CLASS:

R1 Mild

BUSHFIRE CLASS:

NIL

NORTH POINT:

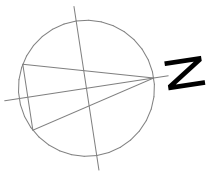

DRAWING TITLE:

Electrical Lower Plan

ISSUE:

Prelim Council

AMENDMENT:

VERSION:

10

SHEET:

9/13

DRAWN BY:

CM

DRAWING SCALE:

1:100

DATE:

21/08/2026

STANDARD ELECTRICAL HEIGHTS

GPO'S

-ALL GPO'S NOT LISTED BELOW ARE TO BE 300mm AFL (UNO)

-KITCHEN BENCH	1050mm
-BREAKFAST BAR (B'BAR)	750mm
-RANGE HOOD (R'HOOD)	1900mm
-MICROWAVE (m/o)	750mm
-REFRIGERATOR (REF)	1900mm
-DISHWASHER (d/w)	300mm
-WASHING MACHINE (w/m)	1050mm
-LAUNDRY BENCH	1050mm
-VANITIES	1050mm

INTERNAL/ EXTERNAL LIGHTS

-LIGHT SWITCHES ARE TO BE INSTALLED AT 1300mm AFL (UNO)

-WALL MOUNTED LIGHTS ARE TO BE INSTALLED AT 2000mm AFL (UNO)


CONNECTIVITY

-TV POINTS ARE TO BE INSTALLED AT 400mm AFL DIRECTLY ABOVE THE CLOSEST GPO (UNO)

-PHONE POINTS ARE TO BE INSTALLED AT 1150mm AFL DIRECTLY ABOVE THE CLOSEST GPO (UNO)

-DATA POINTS ARE TO BE INSTALLED AT 400mm AFL DIRECTLY ABOVE THE CLOSEST GPO (UNO)

(HEIGHTS SPECIFIED ARE TO THE CENTRE LINE OF THE ELECTRICAL FIXTURE)

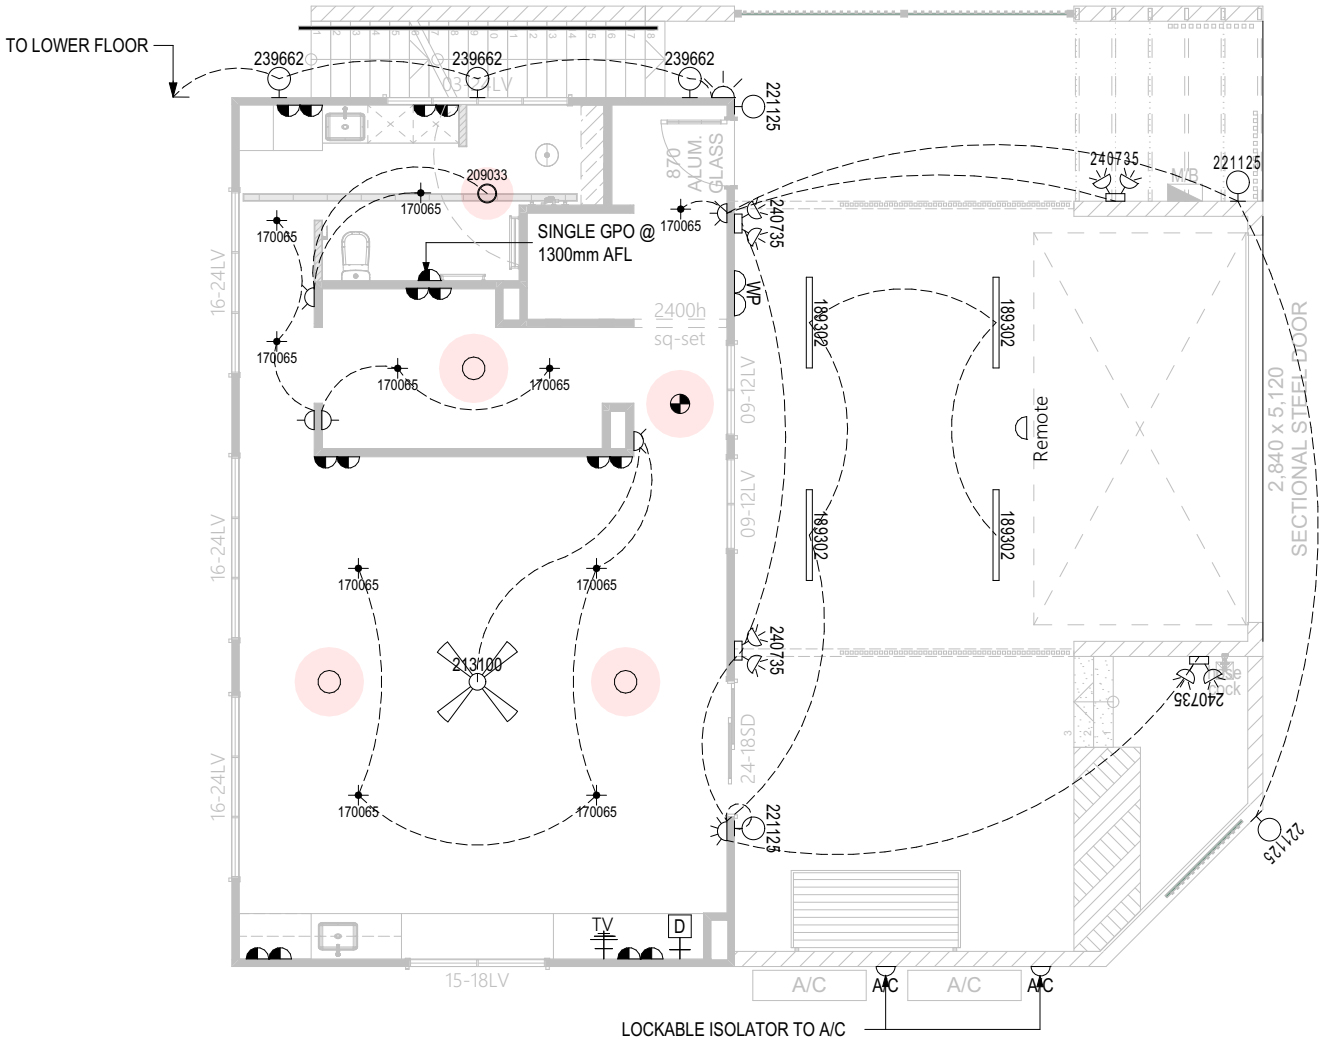

Electrical		
Electrical Item	Symbol	Quantity
170065 - Eclipse Maxi LED Colour Switch DL - White	170065	35
189302 - 1200mm LED Batten - White	189302	4
209033 - Reef 200mm Round Exhaust Fan - White	209033	2
213100 - Aria 132cm Fan with Wall Control - White	213100	2
213182 - Atlanta 142cm Fan and Light with Remote - White	213182	2
221125 - Sunset Illumo Solar LED Sensor Wall Light - Black	221125	4
239662 - Wanaka 2 Light Adjustable Wall Light - White	239662	3
240735 - Sentinel 2 Light Spotlight with Sensor - Black	240735	7
AC Vent - Round		6
Datapoint		3
Double GPO		20
Double GPO Weather Proof		7
Exhaust Vent		1
Garage Remote	Remote	1
Light Switch - Double		4
Light Switch - Four		2
Light Switch - Single		5
Light Switch - Triple		2
Sensor		1
Single GPO		2
Single GPO Weather Proof		1
Smoke Alarm		2
TV Point		3
Weather Proof Isolator Switch - Air Conditioning		2



GENERAL NOTES:

1. Do not scale from drawings.
2. All dimensions to be checked on site.
3. Discrepancies to be reported to author.
4. Dimensions take precedence.
5. Boundaries to be verified by surveyor.
6. Other consultants drawings take precedence.

COPYRIGHT:

These plans are copyright in whole & in part to InspireMeNow Pty Ltd & may not be used or reproduced without written permission

CLIENT NAMES:

Joanne Louise Redburn

STREET No.:

76

LOT:

76

DP:

SP245114

STREET ADDRESS:

Annie Street, AUCHENFLOWER, QLD, 4066

LOCAL GOVERNMENT AUTHORITY:

Brisbane City Council

JOB NUMBER:

BR250157

DESIGN TYPE:

Design By Others

FACADE:

Design By Others

DESIGNER:

ER

COLOUR SCHEME:

N/A

SITE CLASS:

S-P

WIND CLASS:

N3


ENVIRO. EXPOSURE CLASS:

R1 Mild

BUSHFIRE CLASS:

NIL

NORTH POINT:

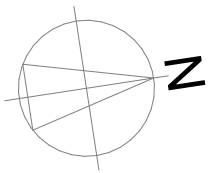

DRAWING TITLE:

Electrical Upper Plan

ISSUE:

Prelim Council

AMENDMENT:

VERSION:

10

SHEET:

10/13

DRAWN BY:

CM

DRAWING SCALE:

1:100

DATE:

21/08/2026

Services

- 1. All service locations are to be determined by the relevant authority and established by an appropriately accredited and insured contractor.
- 2. Stormwater management system is to be installed in accordance with the engineers details and all local government authority requirements.
- 3. Where required onsite waste management systems are to be installed in accordance with a effluent disposal system design prepared by a suitably qualified consultant and all local government authority requirements.

Site Management

- 1. Erosion and sedimentation controls are to be established in accordance with NSW Landcom publication "Managing Urban Stormwater: Soils and Construction - Volume 1, Landcom 2004" and all local government authority requirements.
- 2. All construction waste must be contained on the subject land in a suitable waste enclosure and disposed of at a facility that may lawfully accept the waste.
- 3. Building materials are to be delivered directly onto the subject land and all public reserves are to be maintained clear of rubbish, building materials and all other items.

HEALTH AND SAFETY

Falls, Slips and Trips

During construction, wherever possible, components for this building should be prefabricated off-site or at ground level to minimise the risk of workers falling more than two metres. However, construction of this building will require workers to be working at heights where a fall of more than two metres is possible, and injury is likely to result from such a fall. The builder should provide a suitable barrier wherever a person is required to work in a situation where falling more than two metres is a possibility.

Steps, Loose Objects and Uneven Surfaces

Due to design restrictions for this building, steps or ramps are included in the building, which may be a hazard to workers carrying objects or otherwise occupied. Steps should be clearly marked with both visual and tactile warnings during construction, maintenance, or demolition. The building owners and occupiers should monitor the pedestrian accessways and access to an area where maintenance is routinely conducted to ensure that surfaces have not moved or cracked so that they become uneven and present a trip hazard. Spills, loose material, stray objects, or any other matter that may cause a slip or trip hazard should be cleaned or removed from access ways. Contractors must maintain a tidy worksite during construction, maintenance, or demolition to reduce the risk of trips and falls in the workplace. Materials for construction or maintenance should be stored in designated areas away from access ways and work areas.

Synthetic Mineral Fibre

Fibreglass, Rockwool, ceramic, and other material used for thermal, or sound insulation may contain synthetic mineral fibres, which may be harmful if inhaled or if it comes into contact with the skin, eyes, or other sensitive parts of the body. Personal Protective Equipment (PPE), including protection against inhalation of harmful material, should be used when installing, removing, or working near bulk insulation material.

Falling Objects

- Construction, maintenance, or demolition work on or around this building will likely involve persons working above ground level or floor level. Where this occurs, one or more of the following measures should be taken to avoid objects falling from the area where the work is being conducted onto persons below:
- Prevent or restrict access to the area below where the work is being conducted.
 - Provide toe boards to scaffolding or work platforms.
 - Provide protective structures below the work area.
 - Ensure that all persons below the work area have appropriate Personal Protective Equipment (PPE).

Building Components

During construction, renovation, or demolition of this building, parts of the structure, including fabricated steelwork, heavy panels, and many other components, will remain standing prior to or after supporting parts are in place. Contractors should ensure that temporary bracing or other required support is always in place when collapse, which may injure persons in the area is a possibility.

Services

A rupture of services during excavation or other activity creates various risks, including the release of hazardous material. Where known existing services are located on or around this site, these are identified on the plans, but the exact location and extent of the services may vary from that indicated. Services should be located using an appropriate service (such as Dial Before You Dig), appropriate excavation practice should be used, and, where necessary, specialist contractors should be used.

Locations with underground power:

Underground power lines may be located in or around this site. All underground power lines must be disconnected or carefully located, and adequate warning signs used prior to any construction maintenance or demolition commencing.

Locations with overhead power lines:

Overhead power lines may be near or on this site, and these pose a risk of electrocution if struck or approached by lifting devices or other plant or persons working above ground level. Where there is a danger of this occurring, power lines should be where practical, disconnected or relocated. Where this is not practical, adequate warning in the form of bright coloured tape or signage should be used, or a protective barrier provided.

Manual Tasks

Components within this design with a mass of more than 25kg should be lifted by two or more workers or by a mechanical lifting device. Where this is not practical, suppliers or fabricators should be required to limit the mass of the component. All material packaging, building and maintenance components should clearly show the total mass of packages and where practical, all items should be stored onsite in a way that minimises bending before lifting. Advice should be provided on safe lifting methods in all areas where lifting may occur. Construction, maintenance, and demolition of this building will require the use of portable tools and equipment. These should be fully maintained in accordance with the manufacturer's specifications and not used where faulty or (in the case of electrical equipment not carrying a current electrical safety tag). All safety guards or devices should be regularly checked, and Personal Protective Equipment (PPE) should be used in accordance with the manufacturer's specifications.

Hazardous Substances

Asbestos:

For alteration to a building constructed prior to 1990, the building will likely contain asbestos either in cladding or fire-retardant insulation material. In either case, the builder should check and, if necessary, take appropriate action before demolishing, cutting, sanding, drilling, or otherwise disturbing or creating powdered material.

Volatile Organic Compounds:

Many types of glue, solvents, spray packs, paints, varnishes, and some cleaning materials and disinfectants have dangerous emissions. Areas, where these are used should be kept well ventilated while the material is being used and for a period after installation. The manufacturers' recommendations for use must be carefully always considered.

Confined Spaces

Excavation:

Construction of this building and maintenance on the building will require excavation and installation of items within excavations. Where practical, installation should be conducted using methods that do not require workers to enter the excavation. Where this is not practical, adequate support for the excavation should be provided to prevent collapse. Warning signs and barriers to prevent accidental or unauthorised access to all excavations should be provided.

Enclosed Spaces:

Enclosed spaces where maintenance or other access may be required may present a risk to persons entering for construction, maintenance, or other purposes. Warning signs and barriers to prevent unauthorised access are to be used and maintained throughout the life of the building. Where workers are required to enter enclosed spaces, air testing equipment and Personal Protective Equipment (PPE) should be provided.

Public Access

Public access to construction and demolition sites and areas under maintenance causes a risk to workers and the public. Warning signs and secure barriers to unauthorised access should be provided. Where electrical installations, excavations, plant, or loose materials are present, they should be secured when not fully supervised.

Other High-Risk Activity

All electrical work should be conducted in accordance with the code of practice: Managing Electrical Risks at the Workplace, AS/NZ3012-2019, and all licensing requirements. All work using plant should be conducted in accordance with the code of practice: Managing Risks of Plant at the Workplace. All work should be conducted in accordance with the code of practice: Managing noise and preventing hearing loss at work. Due to the history of serious incidents, it is recommended that particular care be exercised when undertaking work involving steel construction and concrete placement. All the above applies.



CLIENT NAMES:
Joanne Louise Redburn

STREET No.:
76

LOT:
76

DP:
SP245114

SITE ADDRESS:
Annie Street, AUCHENFLOWER, QLD, 4066

LOCAL GOVERNMENT AUTHORITY:
Brisbane City Council

DESIGN TYPE:
Design By Others

JOB NUMBER:
BR250157

FAÇADE:
Design By Others

DESIGNER:
ER

COLOUR SCHEME:
N/A


ENVIRO. EXPOSURE CLASS:
R1 Mild

SITE CLASS:
S-P

BUSHFIRE CLASS:
NIL

WIND CLASS:
N3

GENERAL NOTES:
1. Do not scale from drawings.
2. All dimensions to be checked on site.
3. Discrepancies to be reported to author.
4. Dimensions take precedence.
5. Boundaries to be verified by surveyor.
6. Other consultants drawings take precedence.

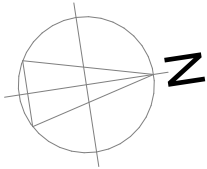NORTH POINT:


DRAWING TITLE:
Health & Safety

ISSUE:
Prelim Council

AMENDMENT:

VERSION:
10

SHEET:
11/13


DRAWING SCALE:
NOT TO SCALE

DRAWN BY:
CM

DATE:
21/08/2026

COPYRIGHT:
These plans are copyright in whole & in part to InspireMeNow Pty Ltd & may not be used or reproduced without written permission



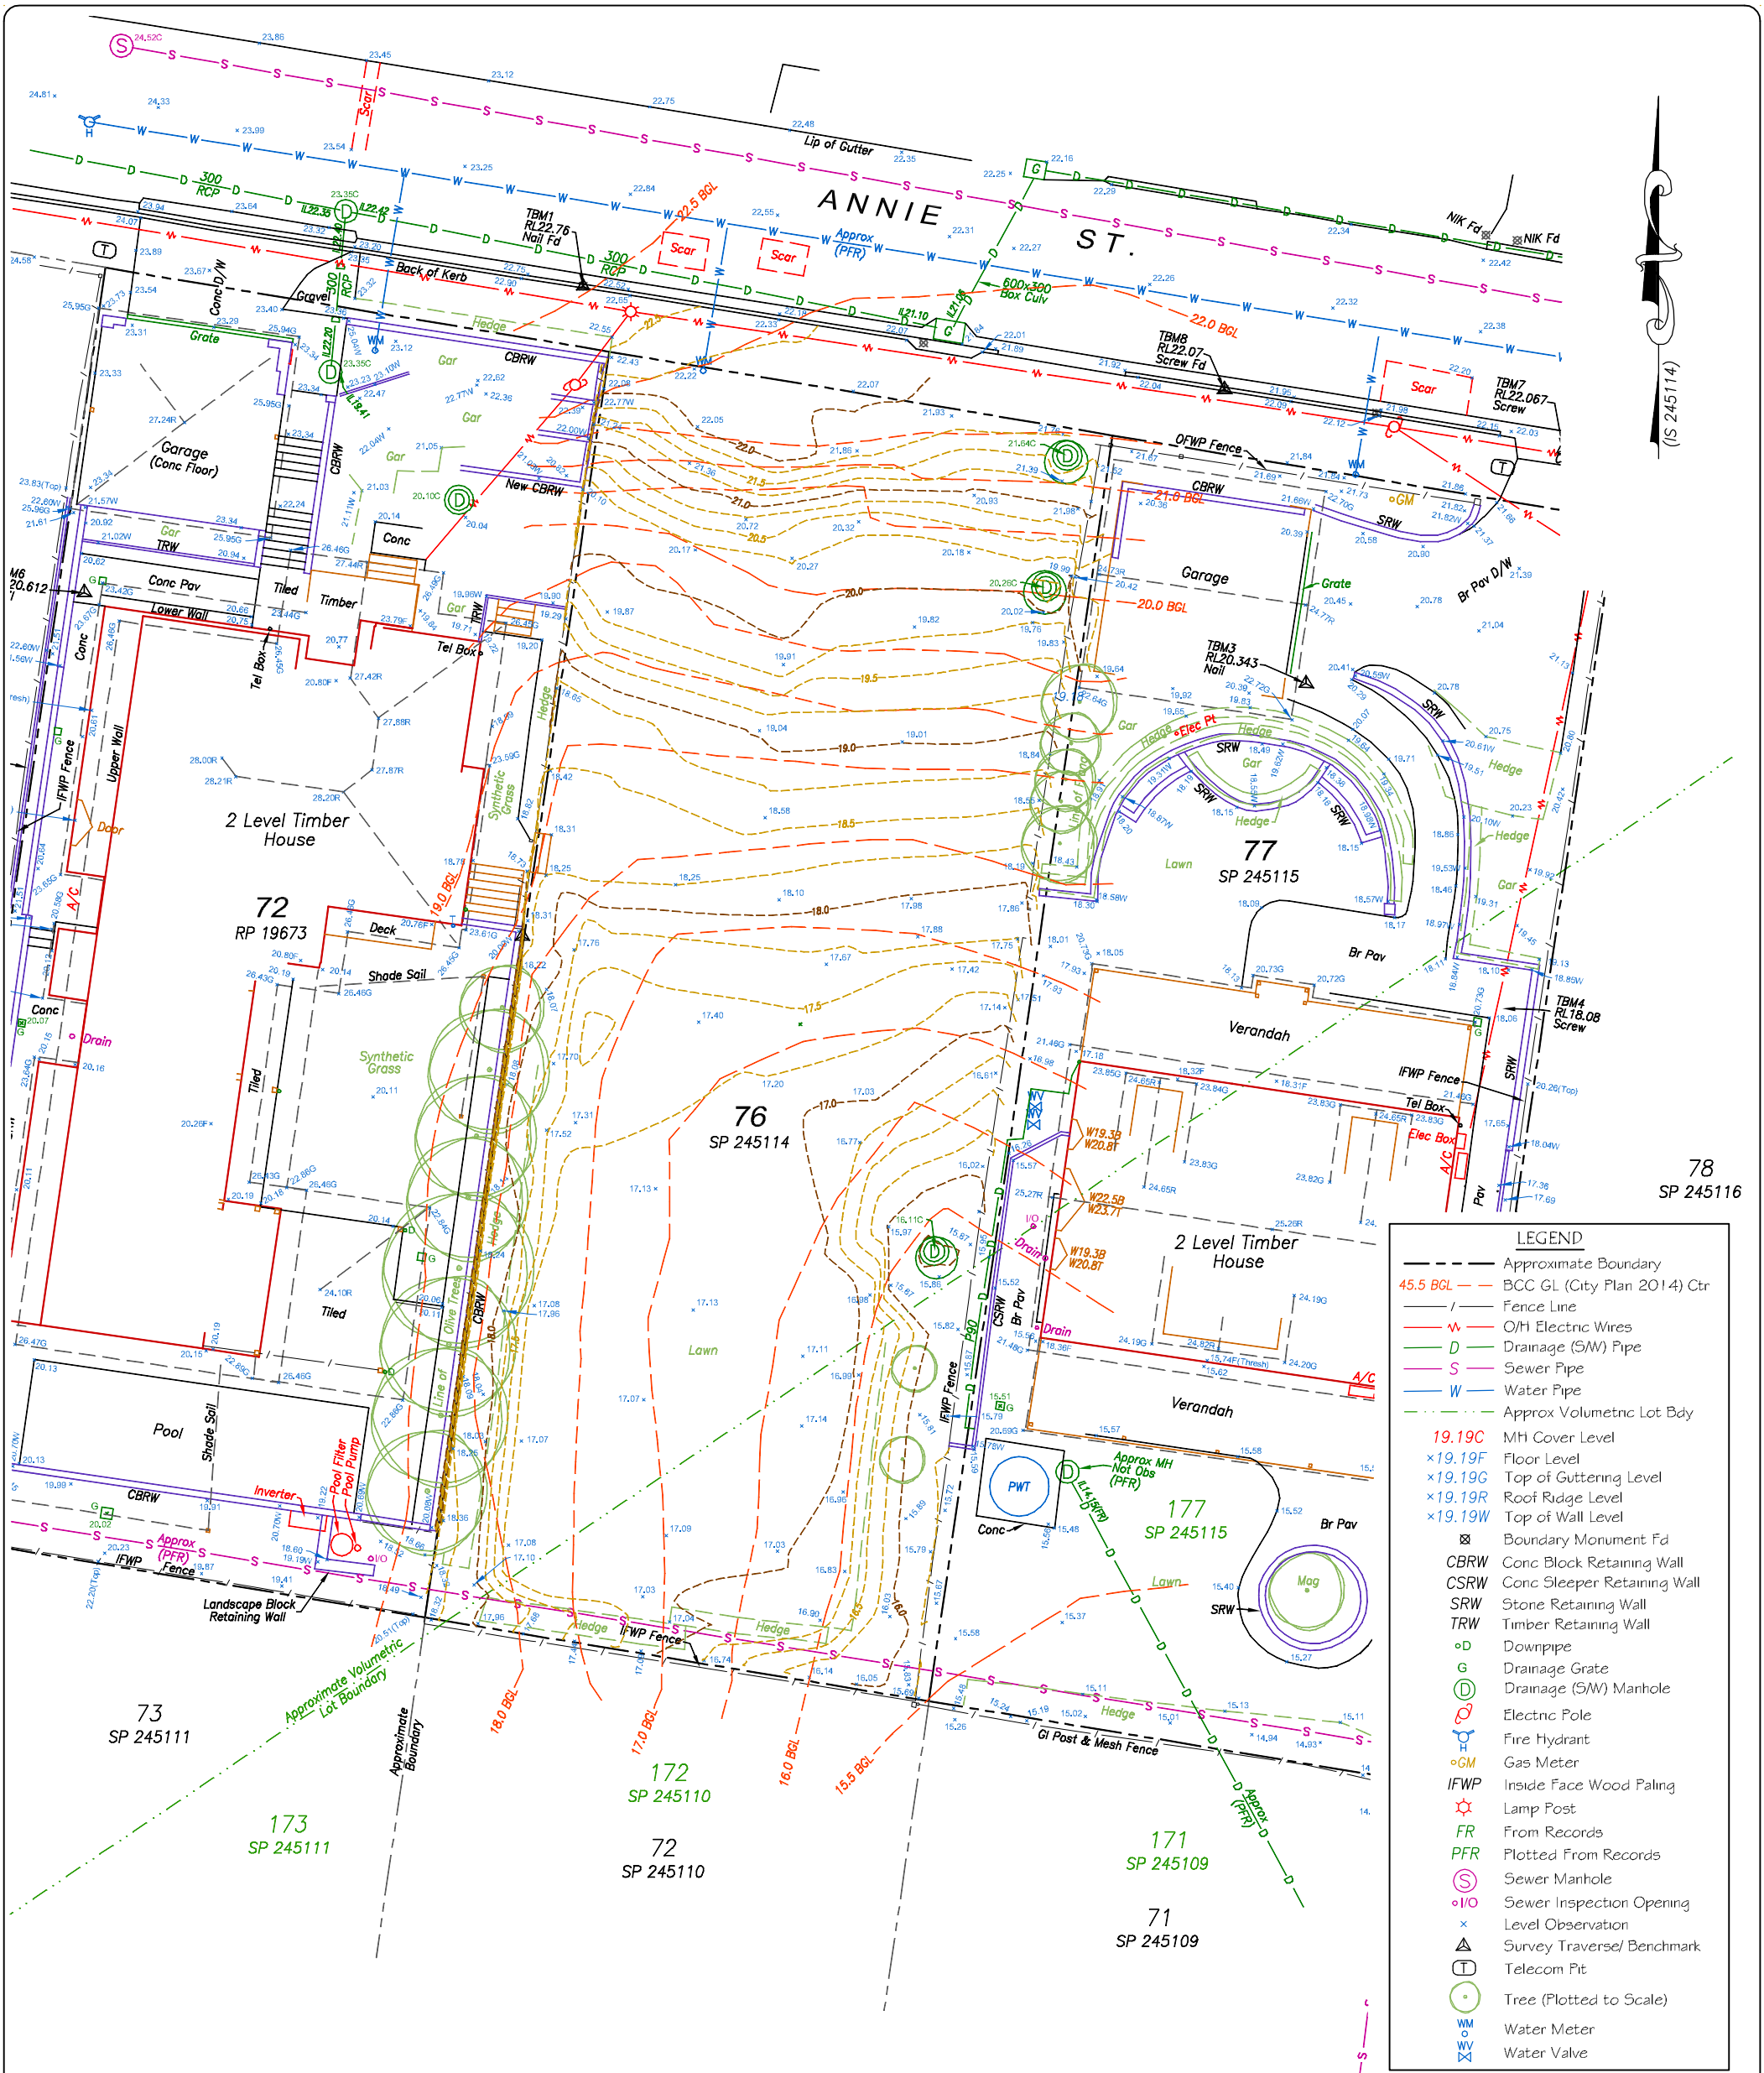

LEGEND	
---	Approximate Boundary
45.5 BGL	BCC GL (City Plan 2014) Ctr
---	Fence Line
W	O/H Electric Wires
D	Drainage (S/W) Pipe
S	Sewer Pipe
W	Water Pipe
---	Approx Volumetric Lot Bdy
19.19C	MH Cover Level
19.19F	Floor Level
19.19G	Top of Gutting Level
19.19R	Roof Ridge Level
19.19W	Top of Wall Level
⊠	Boundary Monument Fd
CBRW	Conc Block Retaining Wall
CSRW	Conc Sleeper Retaining Wall
SRW	Stone Retaining Wall
TRW	Timber Retaining Wall
⊙	Downpipe
⊙	Drainage Grate
⊙	Drainage (S/W) Manhole
⊙	Electric Pole
⊙	Fire Hydrant
⊙	Gas Meter
IFWP	Inside Face Wood Paling
⊙	Lamp Post
FR	From Records
PFR	Plotted From Records
⊙	Sewer Manhole
⊙	Sewer Inspection Opening
⊙	Level Observation
⊙	Survey Traverse/ Benchmark
⊙	Telecom Pit
⊙	Tree (Plotted to Scale)
⊙	Water Meter
⊙	Water Valve

NOTES:
1. ARBITRARY CO-ORDINATES WITH MERIDIAN OF IS245114.
2. LEVEL DATUM IS AHD(0), BASED ON TRANSFER FROM PM158744, WITH PUBLISHED RL 26.840 METRES.
3. BCC GROUND LEVEL (BGL) PRESCRIBED LEVEL (CITY PLAN 2014) FROM ADJUSTED 2002 eBMAP CONTOURS.
4. PROPERTY BOUNDARIES SHOWN ARE APPROXIMATE, BEING BASED ON PLAN DIMENSIONS FROM A LIMITED NUMBER OF OBSERVED BOUNDARY REFERENCE MARKS. IF DESIGNING OR BUILDING CLOSE TO THE BOUNDARIES, OBTAIN AN IDENTIFICATION SURVEY FROM A REGISTERED CADASTRAL SURVEYOR.
5. ONLY OBVIOUS VISIBLE SERVICES HAVE BEEN LOCATED AND SHOWN. NOTIFY AND SEARCH DBYD PRIOR TO ANY EXCAVATION.
6. CONTOUR INTERVAL FOR EXISTING LEVELS IS 0.25 METRES.
7. 22/1/2025 NOTE UPDATED DETAIL AND CONTOURS ONLY FOR LOT 76.

SURVEYING & SPATIAL DATA SOLUTIONS

- DETAIL SURVEYS
- AS-CON
- SETTING OUT
- SERVICE LOCATION
- MONITORING
- MODELLING ...

Q SPATIAL PTY LTD ABN: 212 740 030 58
P.O. Box 232, Ashgrove West, QLD 4060
m. 0468 633 765 e. mark@qspatial.com.au

Scale Bar (Metres)

1:200

THIS DRAWING HAS BEEN PREPARED BY Q SPATIAL FOR A PARTICULAR PURPOSE, WITH APPROPRIATE SCALE AND ACCURACY CONSIDERATIONS. IT SHOULD NOT BE USED FOR ANY OTHER PURPOSE. IT IS ALSO PROTECTED BY COPYRIGHT LAW SUCH THAT REPRODUCTION, BY ANYONE EXCEPT OUR DIRECT CLIENT, REQUIRES PRIOR WRITTEN CONSENT.

RP ADDRESS: Lot 76 on SP245114

CLIENT: Integrity New Homes

DWG TITLE: Contour & Detail Survey			
LOCATION: 76 Annie Street, Auchenflower, Qld.			
LA: BCC	SURV: MQ	DATE: 29/1/25	DRAWN: MQ
A3	SCALE: 1:200	DWG NO: Q865#04	REV: